

LEGENDE :

D.I

:Detecteur d'Incendie

B.A.E.S

:Bloc Autonome d'Eclairage et Secours

Ext

:Extincteur

R.I.A

:Robinet d'Incendie Armé

C


:Commande manuelle de desemfumage

B.A.S

: BAC A SABLE

Toutes les portes (SAS et Cloisonnement) sont des PF 1/2h + ferme porte

DAD détecteur autonome déclencheur

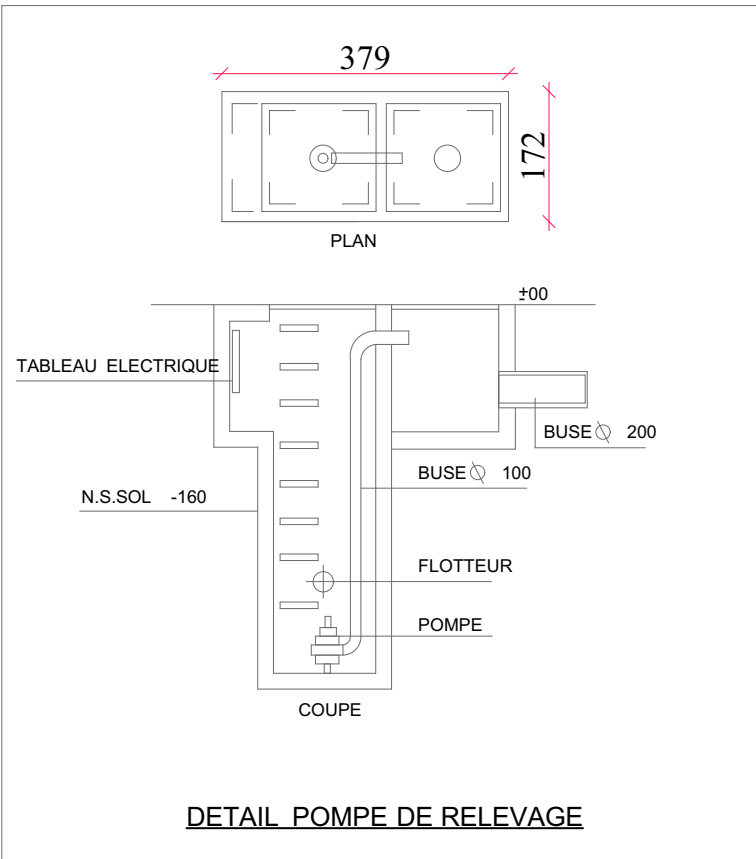

ROYAUME DU MAROC
PROVINCE EL JADIDA
COMMUNE TERRITORIALE D'EL JADIDA


MAITRE D'OUVRAGE :
STE BINAA AL BADIL S.A.R.L
Représenté par : EL KAIM-BILLAH AHMED

PROJET : LOTISSEMENT EN VILLA ET CONSTRUCTION D'UN GROUPEMENT D'HABITATIONS EN SOUS-SOL ET R+2
Sis : Pté DITE : " Ard Feddane" Avenue Jabrane Khalil Jabrane
-EL JADIDA-
T.F 127 938/08

PLANS .
SOUS-SOL

LE MAITRE D'OUVRAGE EST TENU DE PRESENTER A L'ARCHITECTE LE TECHNIQUE PRO ETABLI PAR UN BUREAU D'ETUDE AGREE, ET INFORMER L'ARCHITECTE DE LA DATE DU COMMENCEMENT DES TRAVAUX .

PLANCHE N° :
2 / 5

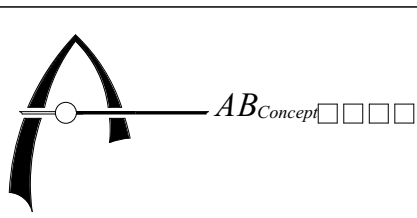

BELARBI ANASS
Architecte d'E.N.A
Bureau n° 1 Bloc " D " Résidence Essouf
-EL JADIDA-
Tél: 0523 39 43 35 Fax: 08 08 33 93 43

MODIFICATION :
ECHELLE : 1/100
DATE LE : 18-05-2026

SOUS-SOL
S= 2851.11 m²

LOT 2	
Surface Terrain	2896,34 m²
Nombre Appart	32
Nombre Commerce	12
CES	44%

Lot B (A construire en Résidence en sous-sol et R+2)

Lot "D" à Régulariser

602,40 m²

12

Administration à construire au RDC de la Residence 3 sur la voie de 20 à céder sans droit à l'indemnisation (suite l'article 5.2 du règlement d'aménagement)

ASSEMBLAGE REZ DE CHAUSSEE
S= 5172 m²

LOT 1	
Surface Terrain	7 456,93 m²
Nombre Appart	107
Nombre Commerce	18
CES	52%

Lot A (A construire en Résidence en sous-sol et R+2)

LEGENDE :

 Détecteur d'intrusion

 Bloc Autonome d'Eclairage et de Sécurité


 Extincteur

 Ruban d'Arrière Arrière

 Commande manuelle de déclenchement

 RAC A SABLE

Toutes les portes (SAS et Châssis) sont des PF 120 - ferme porte
DAD : détecteur autonome de déclenchement

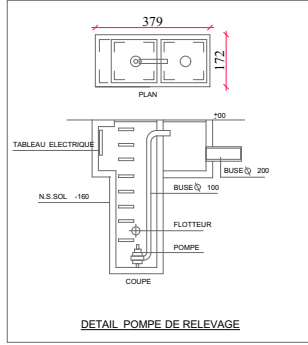

ROYAUME DU MAROC
PROVINCE EL JADIDA
COMMUNE TERRITORIALE D'EL JADIDA

MAITRE D'OUVRAGE :
STE BINAA AL BADIL S.A.R.L
Représenté par : EL KAIM-BILLAH AHMED


PROJET : LOTISSEMENT EN VILLA ET CONSTRUCTION D'UN GROUPEMENT D'HABITATIONS EN SOUS-SOL ET R+2
Sis : Pté DITE : "Ard Feddane" Avenue Jabrane Khalil Jabrane -EL JADIDA-
T.F 127 938/08

PLANS
ASSEMBLAGE REZ DE CHAUSSEE
(RESIDENCE 1-2 et 3)

PLANCHE N° :

3 / 5

LE MAITRE D'OUVRAGE EST TENU DE PRESENTER A L'ARCHITECTE LE TECHNIQUE VTD ETARI PAR UN BUREAU D'ETUDE AGREE ET INFORMER L'ARCHITECTE DE LA DATE DU COMMENCEMENT DES TRAVAUX .

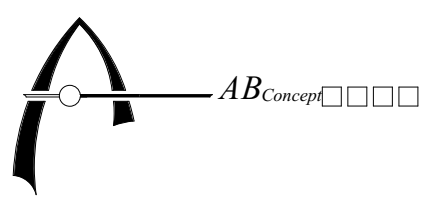

BELARBI ANASS
Architecte d'E.N.A
Bureau n°1 Bloc "D" "Residence Essafie"
-EL JADIDA-
Tél: 0523 39 43 35 Fax: 08 08 35 95 43

MODIFICATION :

ECHELLE : 1/250

DATE LE : 18-05-2026

-TABLEAU RECAPITULATIF DES SURFACES

SOUS-SOL	2851 m²
REZ DE CHAUSSEE	5172 m²
1ER ETAGE	5704 m²
2EME ETAGE	5704 m²
TOTAL	19 431 m²

FONDATIONS



LEGENDE :

- [D1] : Détecteur d'incendie
- [S.A.E.S.] : Bloc Autonome d'Éclairage et Sécurisé
- [E] : Extincteur
- [R.A.A.] : Robot d'Incendie Armé
- [C.M.] : Commande manuelle de déclenchement
- [B.C.A.] : B.C.A. SABLE
- Toutes les portes (SAS et Cloisonnement) sont des PF 1/2h + ferme porte
- DAD : détecteur autonome déclencheur

ROYAUME DU MAROC
PROVINCE EL JADIDA
COMMUNE TERRITORIALE D'EL JADIDA

MAITRE D'OUVRAGE :
STE BINAA AL BADIL S.A.R.L
Représenté par : EL KAIM-BILLAH AHMED


PROJET : LOTISSEMENT EN VILLA ET CONSTRUCTION D'UN GROUPEMENT D'HABITATIONS EN SOUS-SOL ET R+2
Sis : Pté DITE : "Ard Feddane" Avenue Jabrane Khalil Jabrane
-EL JADIDA-
T.F 127 938/08

PLANS.
ETAGE COURANT
(RESIDENCE 1-2 et 3)

LE MAITRE D'OUVRAGE EST TENU DE PRESENTER A L'ARCHITECTE LE TECHNIQUE VRD ETABLI PAR UN BUREAU D'ETUDE AGREE, ET INFORMER L'ARCHITECTE DE LA DATE DU COMMENCEMENT DES TRAVAUX.


PLANCHE N° :

4 / 5

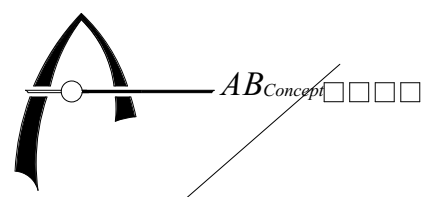


BELARBI ANASS
Architecte d'E.N.A
Bureau n°1 Bloc "D" Residence Essafne
-EL JADIDA-
Fix: 0523 39 43 35 Fax: 08 08 35 93 43


MODIFICATION :
ECHELLE : 1/250
DATE LE : 18-05-2026

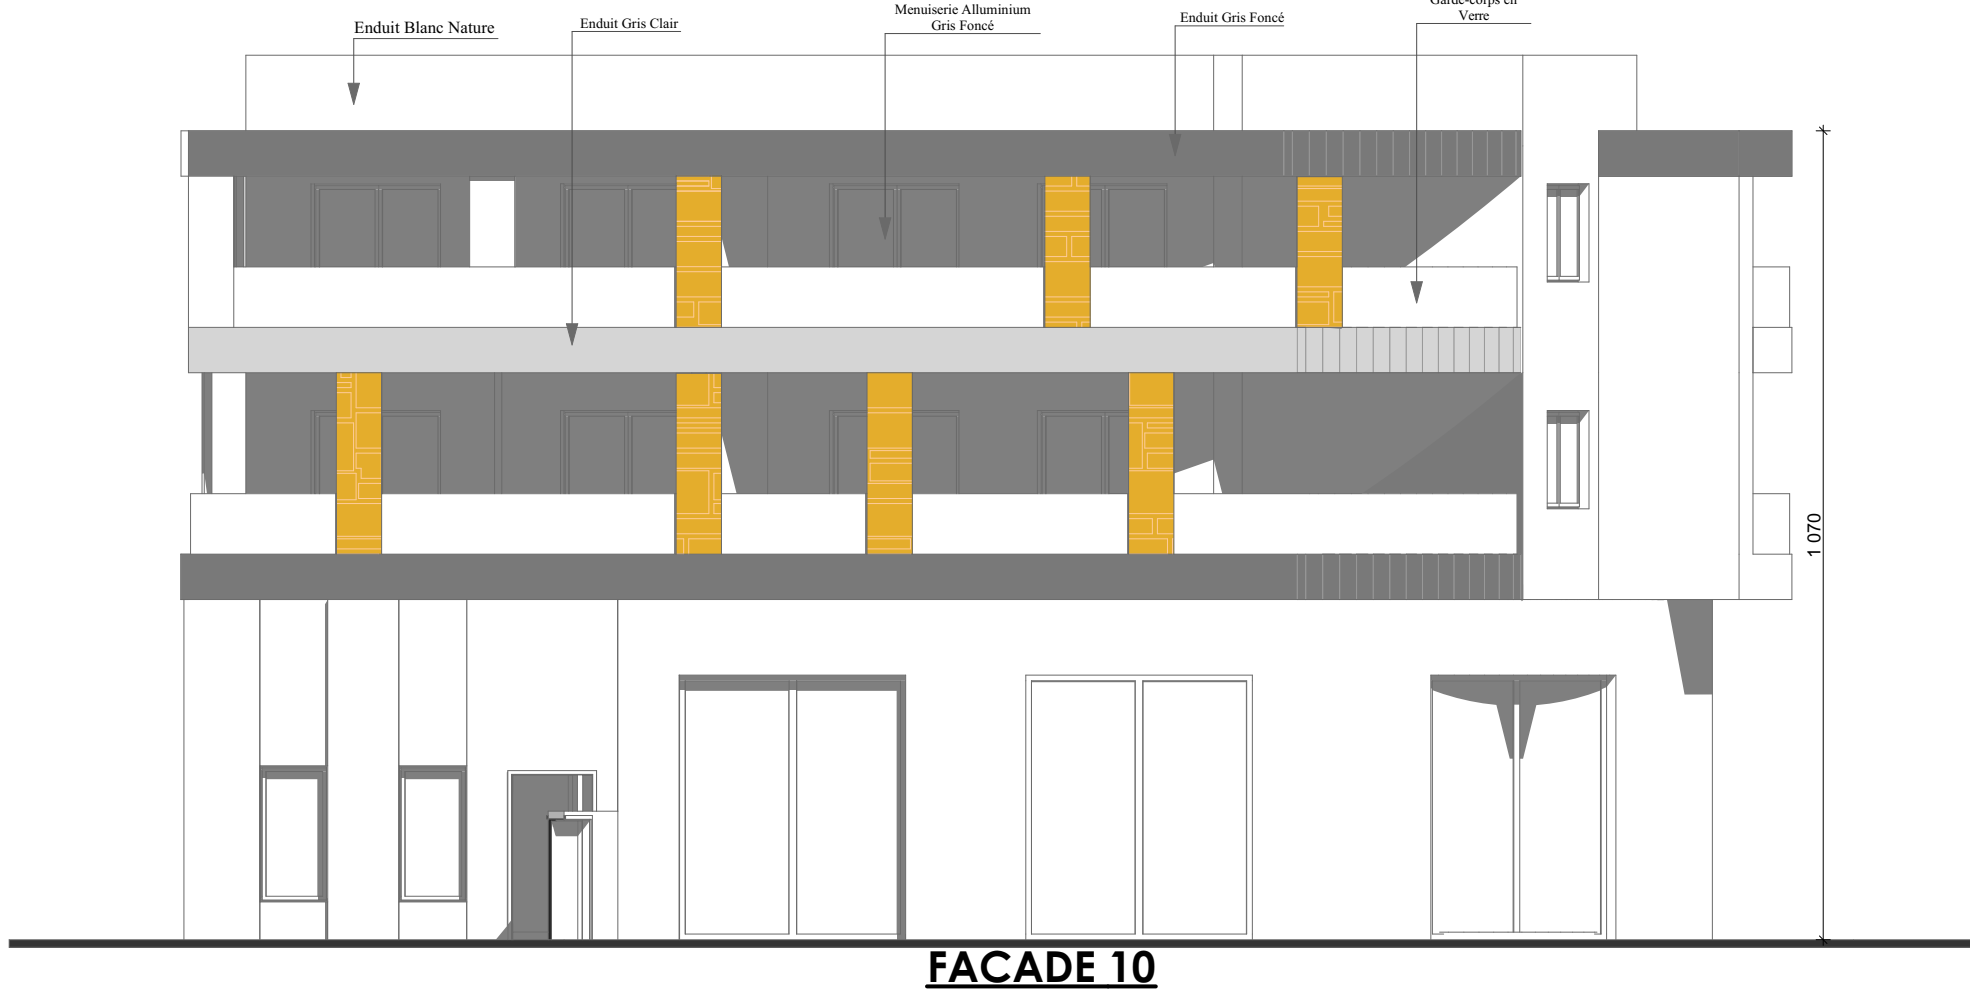


FACADE 10

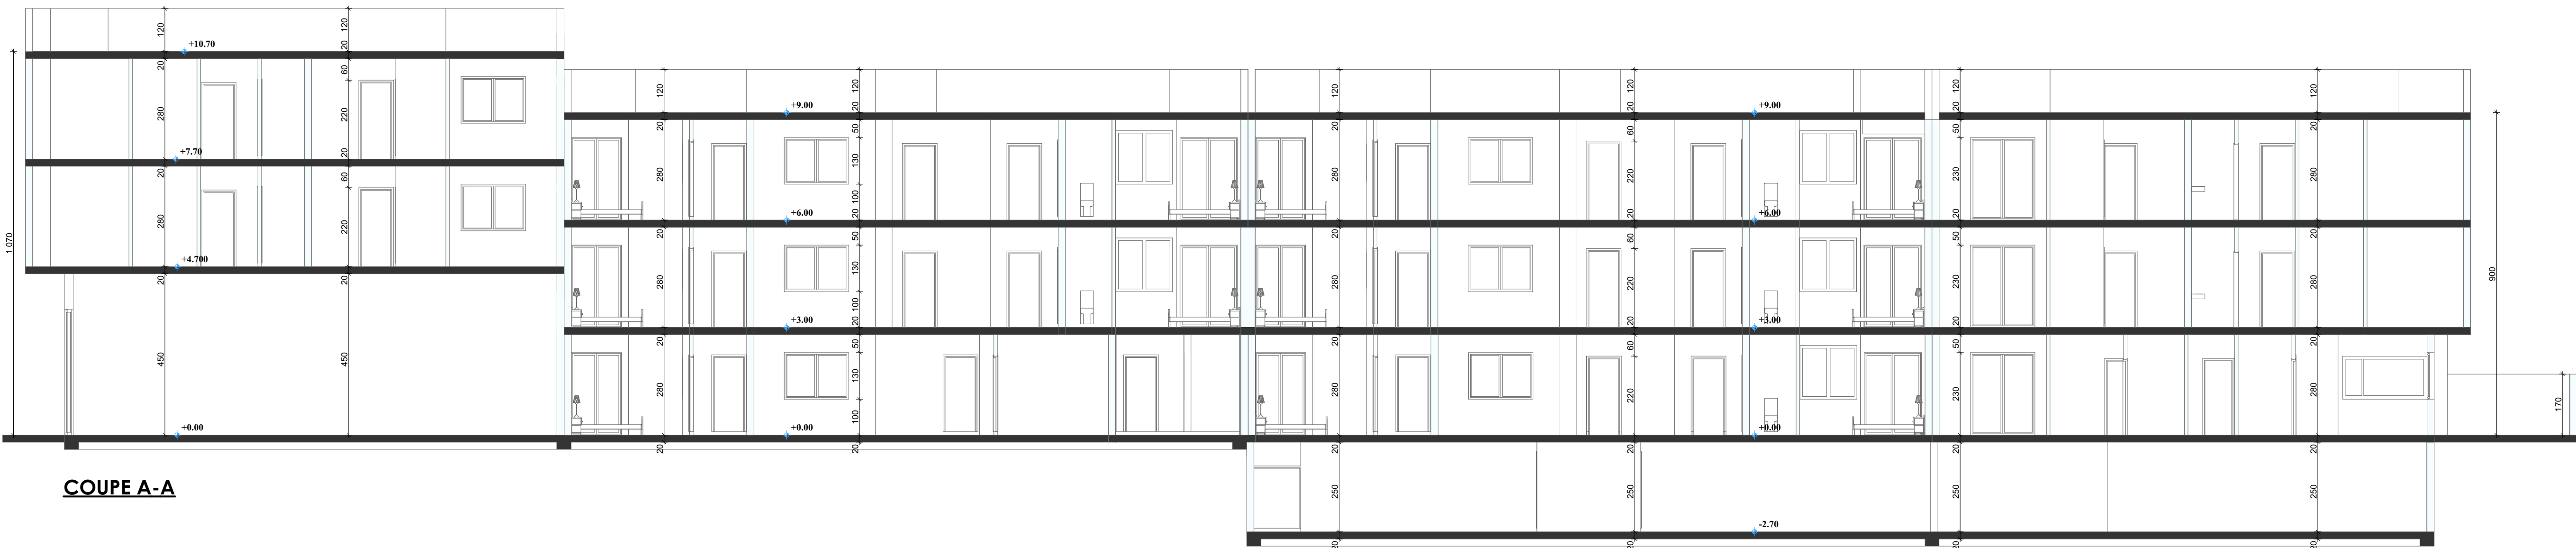


COUPE A-A

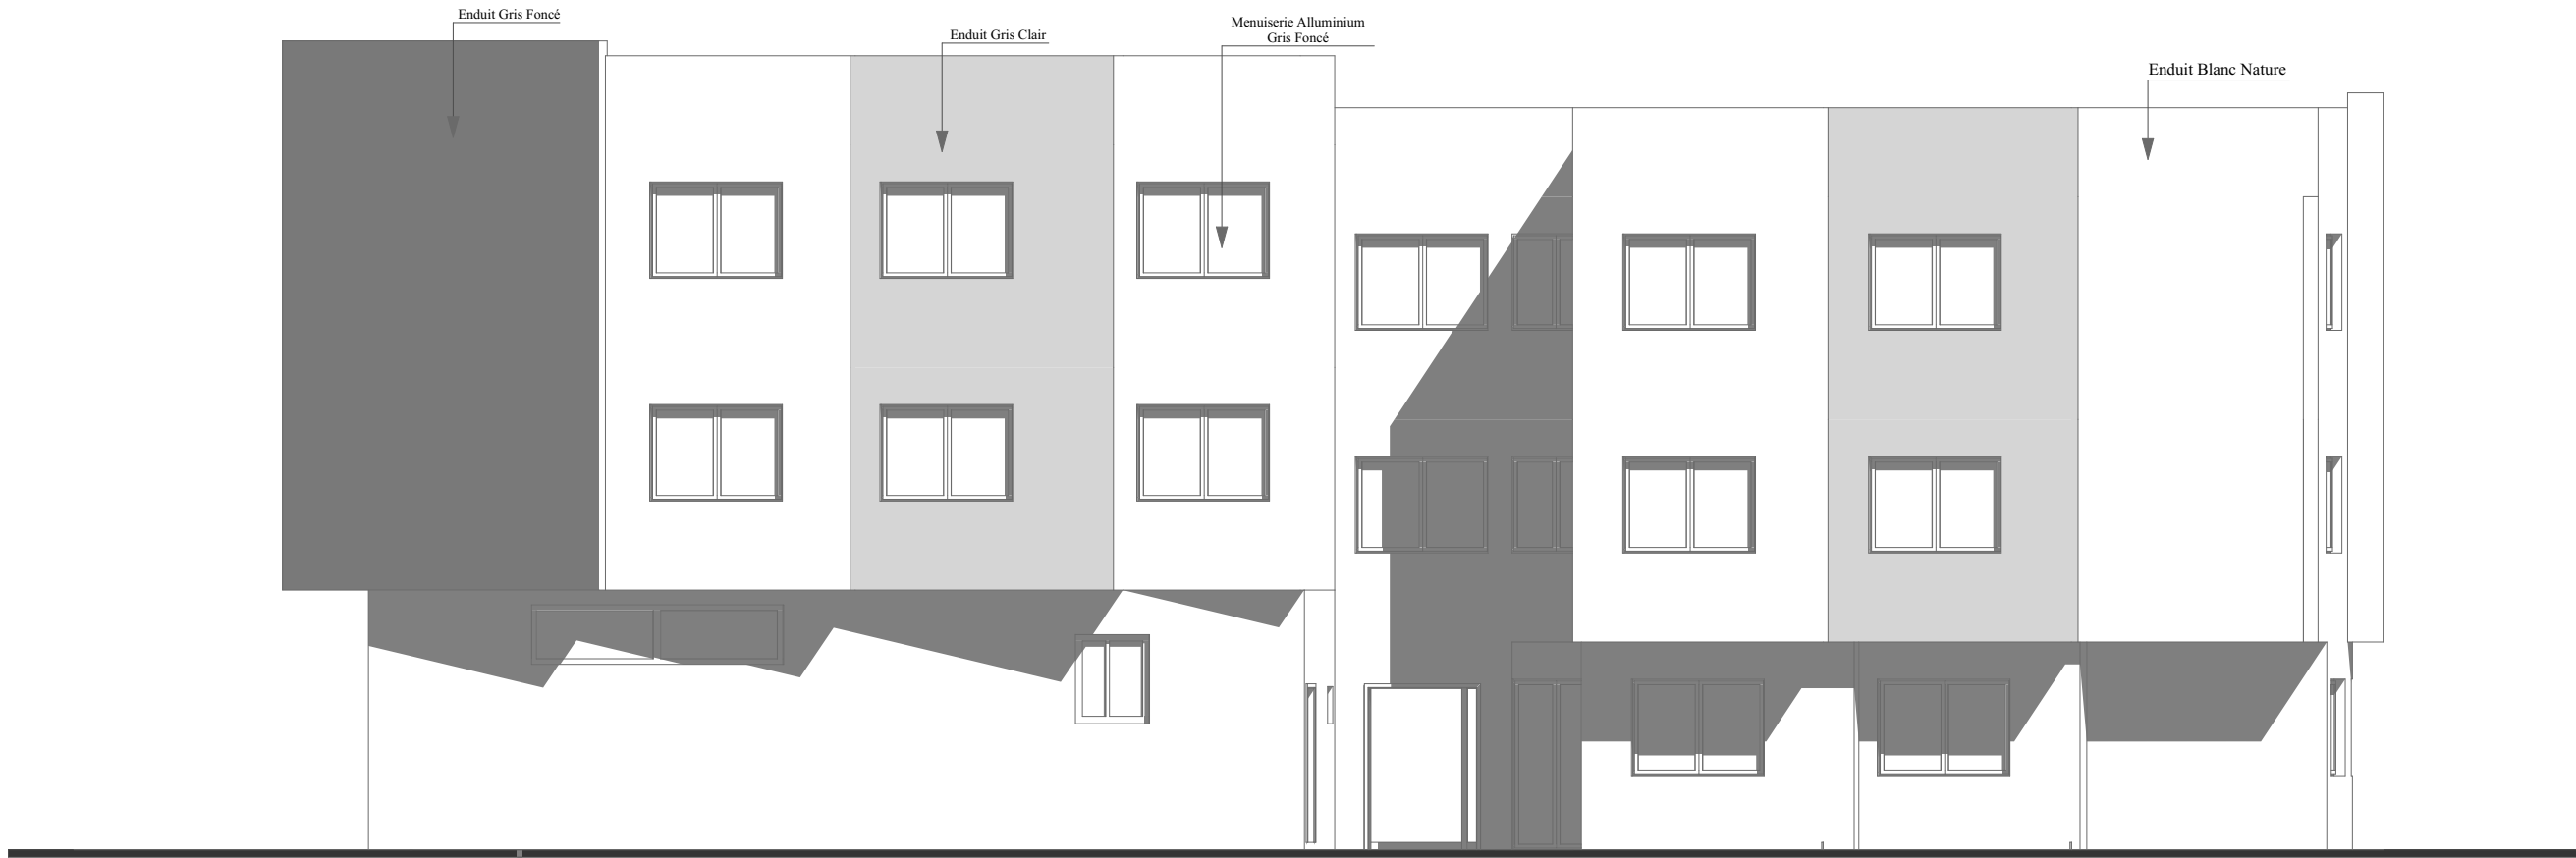

FACADE 8

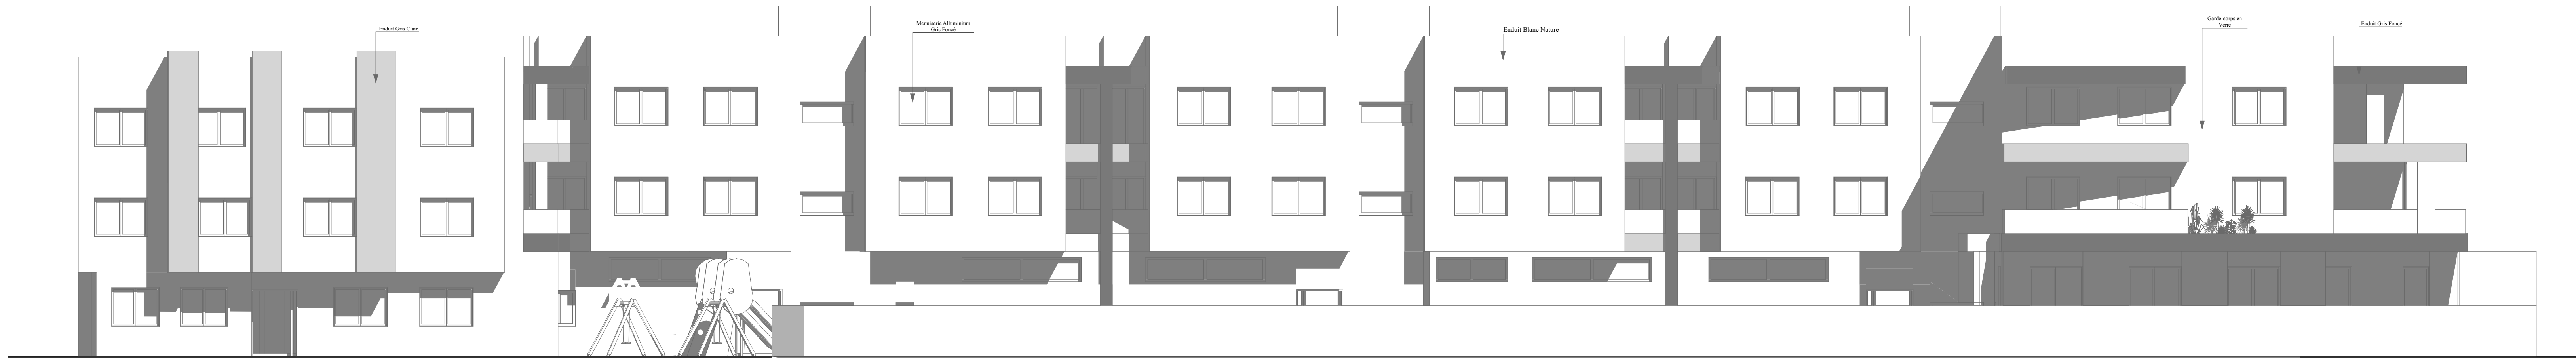

FACADE 9

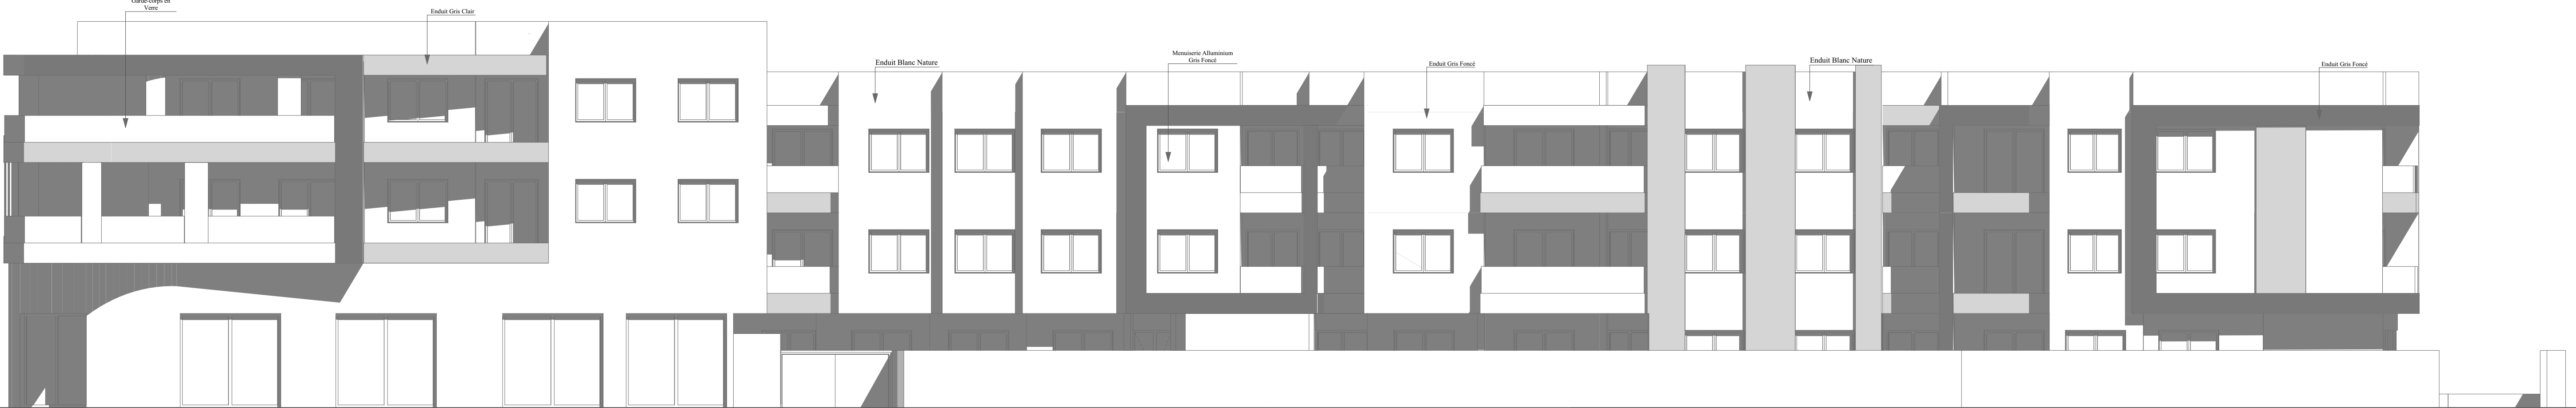


FACADE 6




FACADE 7



FACADE 4

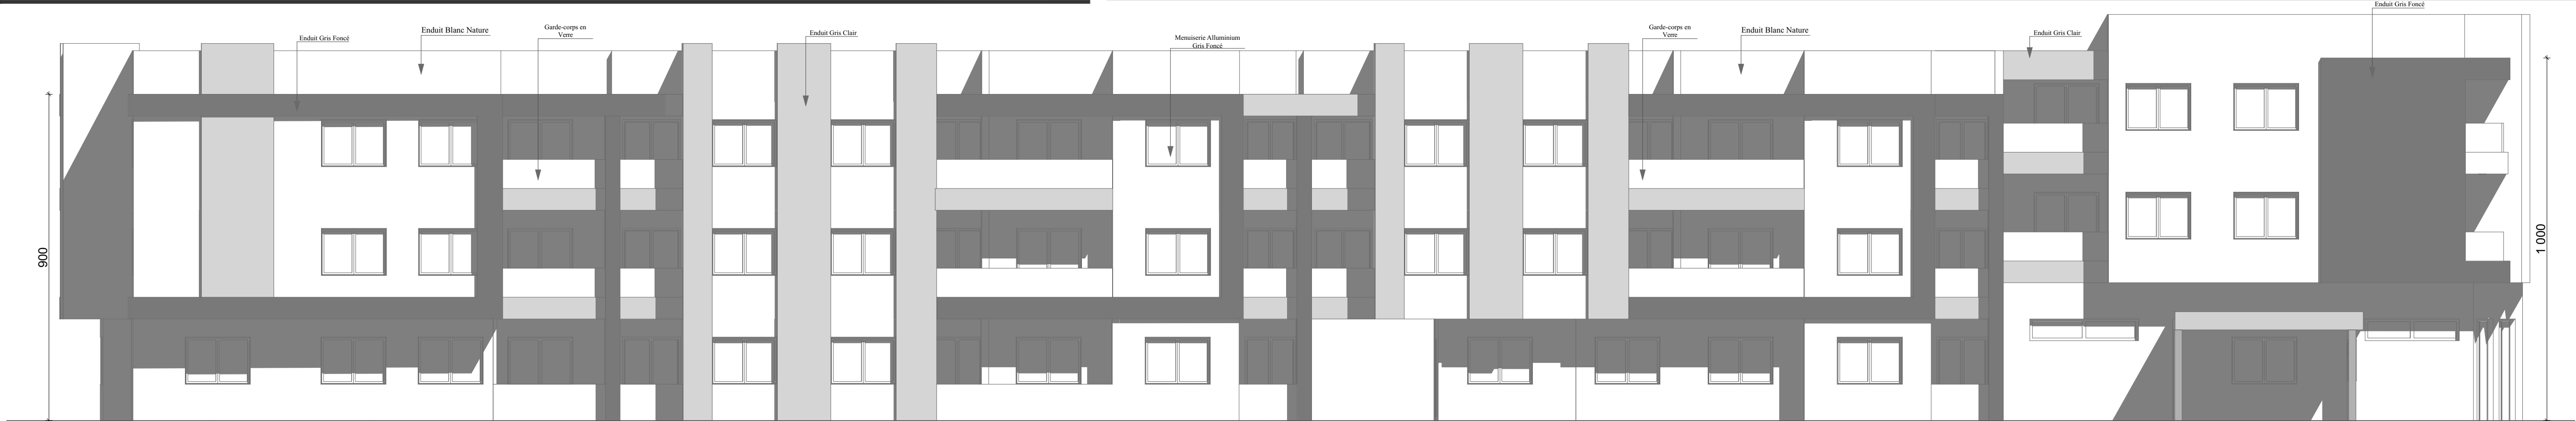


FACADE 5

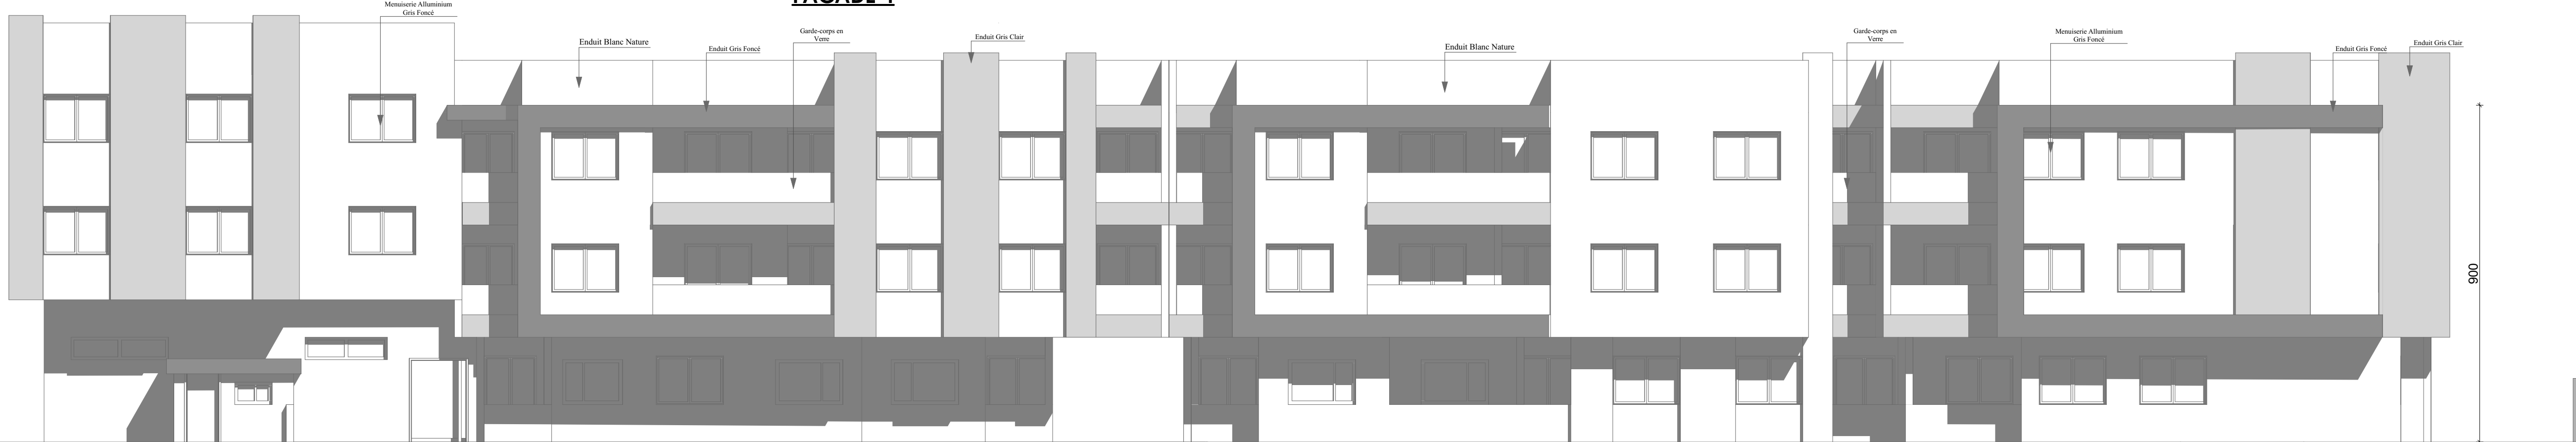

FACADE 2



FACADE 3

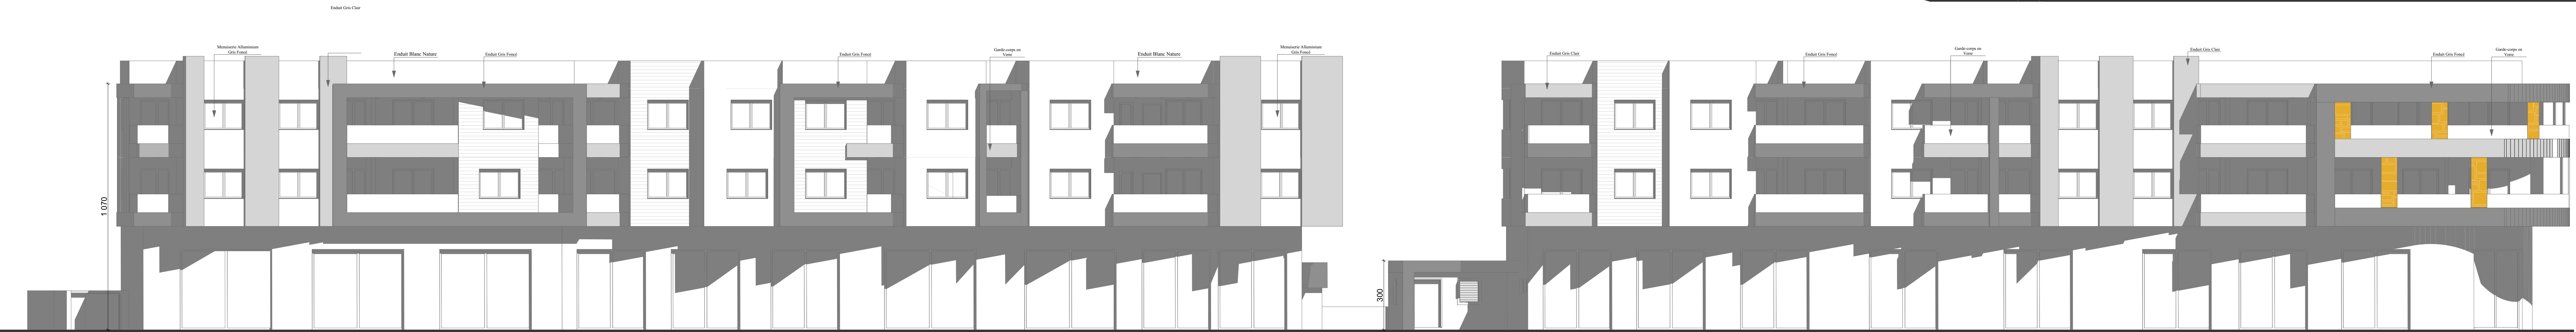

FACADE 1

ROYAUME DU MAROC

PROVINCE EL JADIDA

COMMUNE TERRITORIALE D'EL JADIDA

MAITRE D'OUVRAGE :

STE BINA AL BADIL S.A.R.L

Représenté par : EL KAIM-BILLAH AHMED

PROJET :

LOTISSEMENT EN VILLA ET CONSTRUCTION D'UN GROUPEMENT D'HABITATIONS EN SOUSSOL ET R+2

Sis : Pré DITE : "Ard Feddane" Avenue Jabrane Khalil Jabrane -EL JADIDA-


T.F 127 938/08

PLANS :

LE MAITRE D'OUVRAGE EST TENU DE PRESENTER A L'ARCHITECTE LE TECHNIQUE TRD ETABLI PAR UN BUREAU D'ETUDE AGREE ET D'INFORMER L'ARCHITECTE DE LA DATE DU COMMENCEMENT DES TRAVAUX

PLANCHE N° :

5 / 5

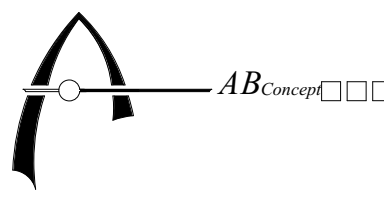

BELARBI ANASS

Architecte d'E.S.A

Bureau d'Etude et de Travaux

EL JADIDA

Projet: 10/21 Pr 41 Pr

Fait: 08/05/2024

MODIFICATION :

ECHELLE : 1/100

DATE LE : 18-05-2026