


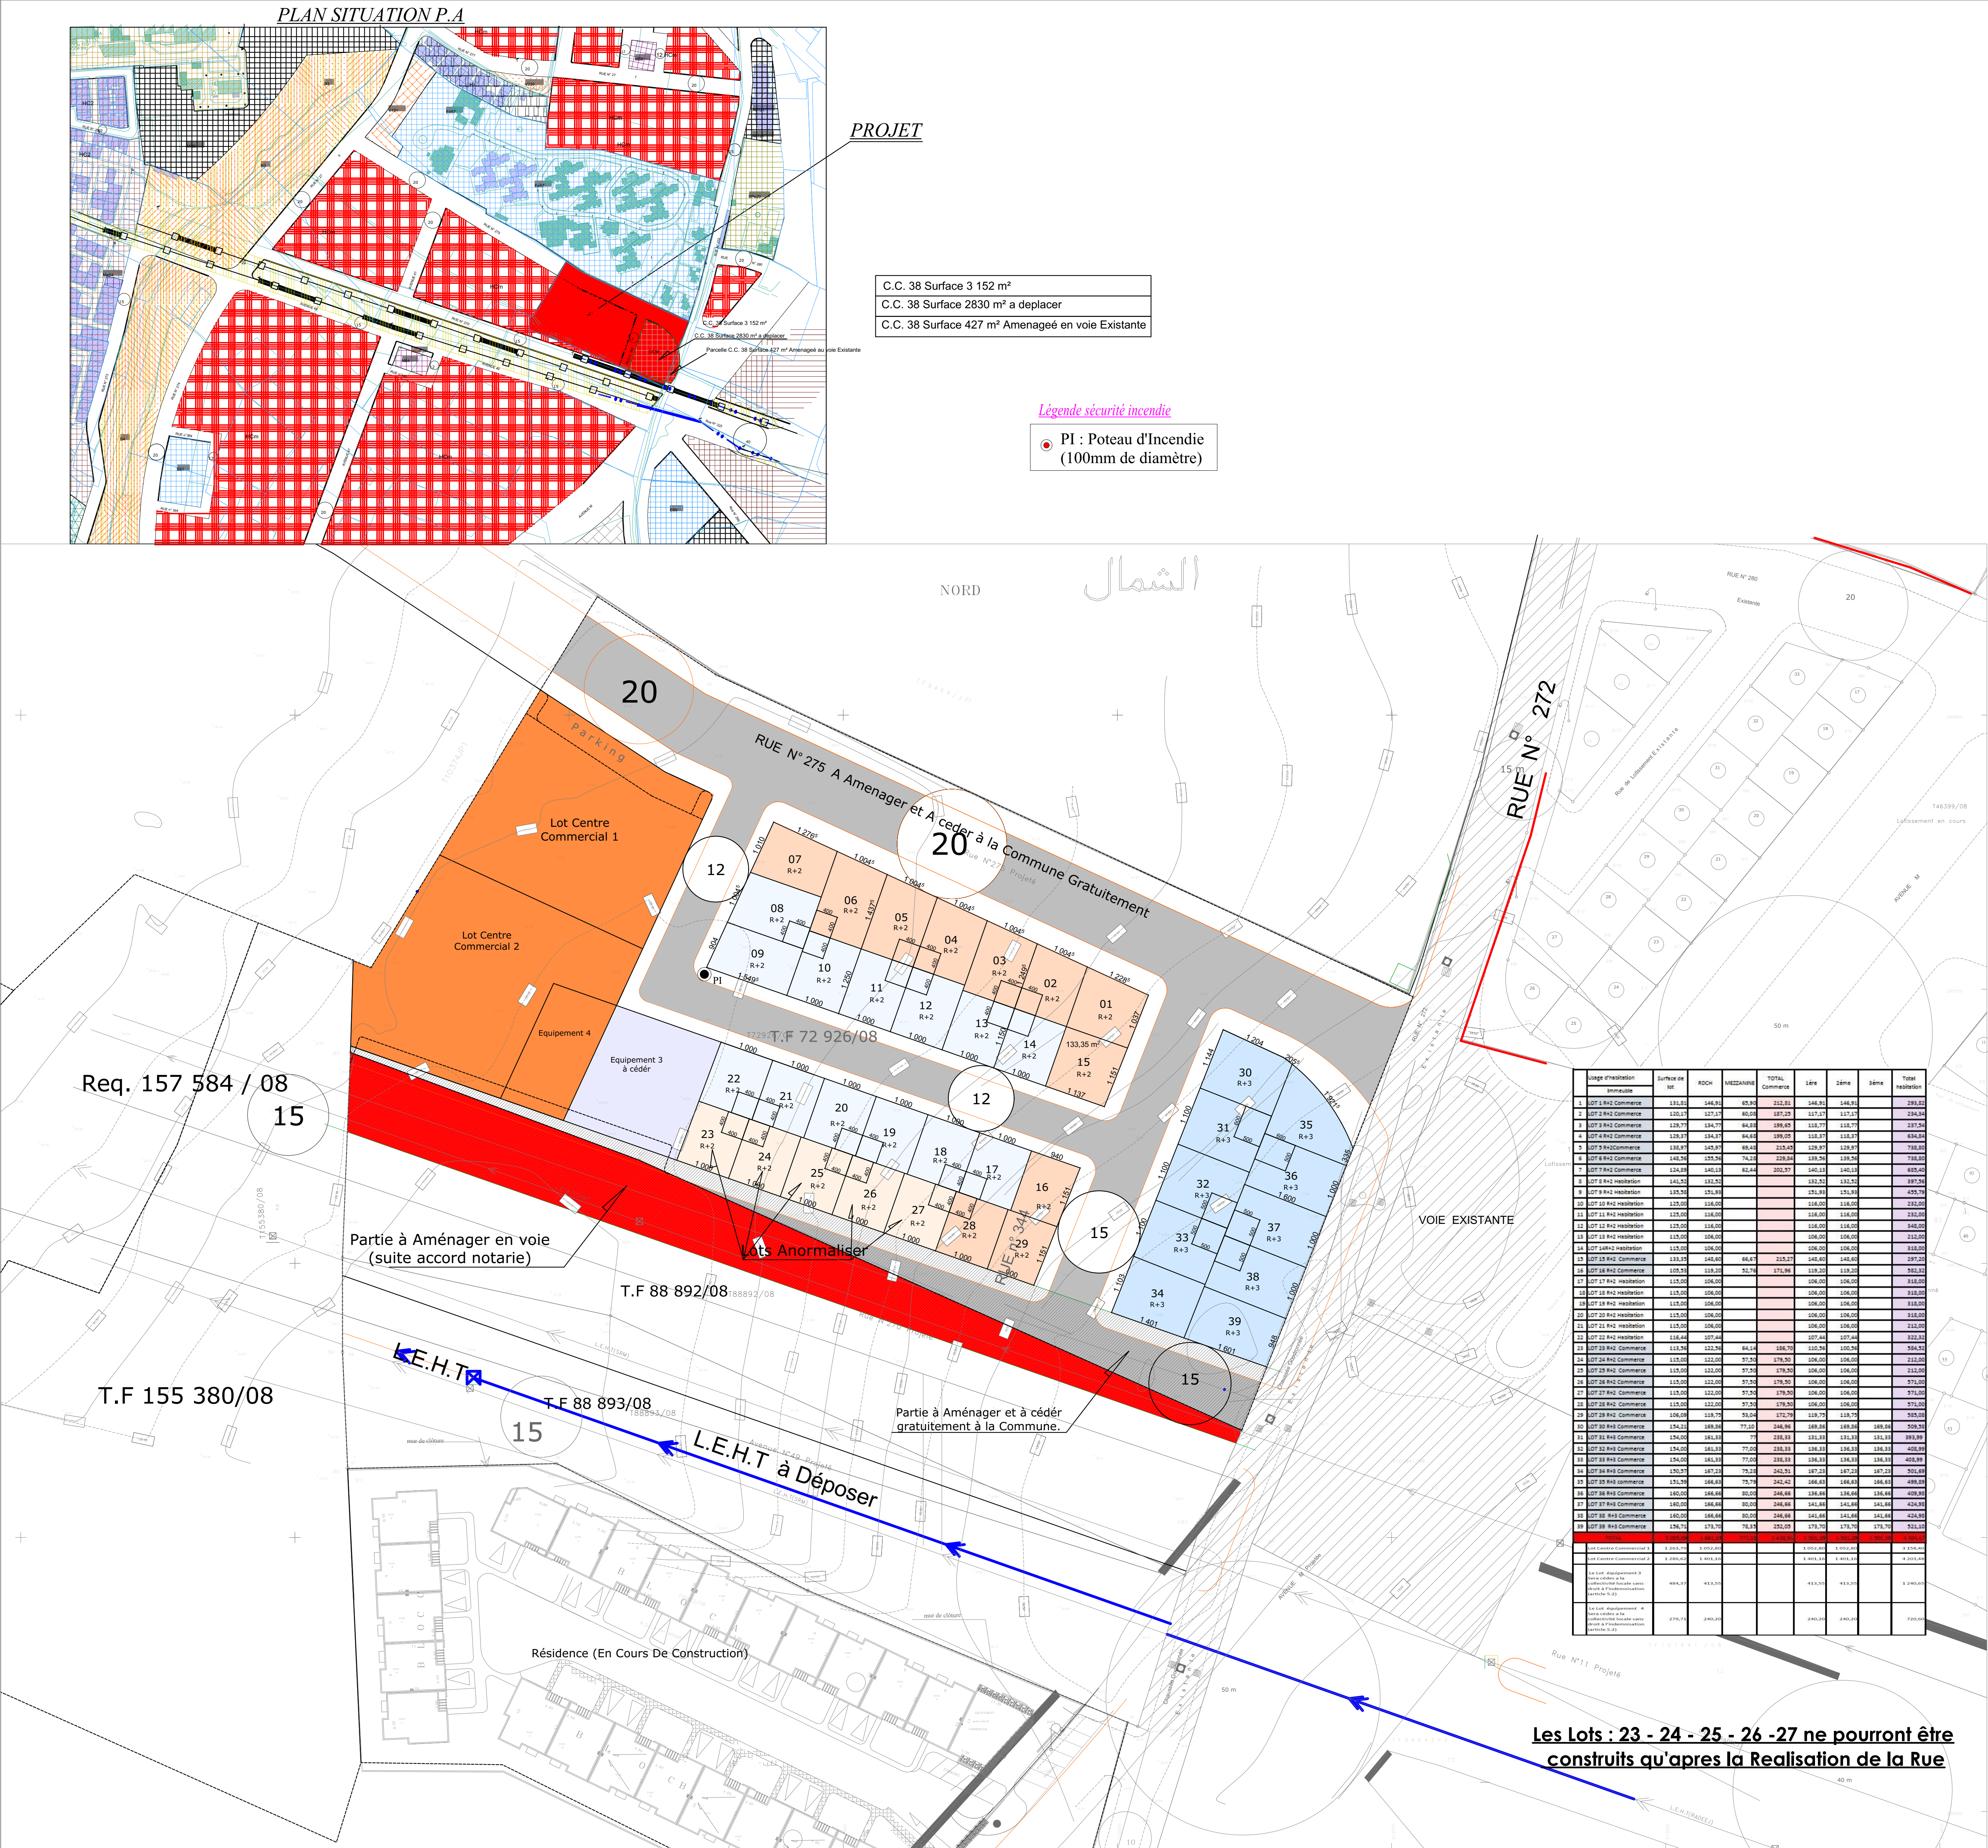

ROYAUME DU MAROC  
PROVINCE D'EL JADIDA  
COMMUNE TERRITORIALE EL JADIDA

MAITRE D'OUVRAGE :  
STE SOUKKANIA GESTION S.A.R.L Représentée par :  
EL Kouhene Mohamed Youssef


PROJET :  
LOTISSEMENT EN R+2 et R+3  
SIS : Pté dite Blad Boukhaima,  
T.F 72 926/08 EL JADIDA

PLANS :

PLAN N° :  
1 / 1

LE MAITRE D'OUVRAGE EST TENU DE PRESENTER A L'ARCHITECTE DES PLANS DE BETON ARME ETABLIS PAR UN BUREAU D'ETUDE AGREE, ET INFORMER L'ARCHITECTE DE LA DATE DU COMMENCEMENT DES TRAVAUX .

MODIFICATION :  
ECHELLE : 1/500  
DATE LE : 13-04-2026

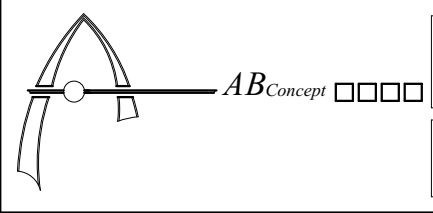

BELARBI ANASS  
Architecte d'E.N.A  
Bureau N° 1 Bloc " D " Résidence Essouf  
EL JADIDA  
Fix : 0523 39 43 33 Fax : 08 35 95 43

| TABLEAU DE CONTENANCE ECONOMIQUE                                   |                |                 |               |                 |
|--------------------------------------------------------------------|----------------|-----------------|---------------|-----------------|
| N°LOT Econ. R+2                                                    | Economique R+2 |                 | Immeuble R+3  |                 |
|                                                                    | SUPERFICIE m²  | N°LOT Econ. R+2 | SUPERFICIE m² | N°LOT Econ. R+3 |
| 01                                                                 | 131.81         | 15              | 133.35        | 30              |
| 02                                                                 | 120.17         | 16              | 105.53        | 31              |
| 03                                                                 | 129.77         | 17              | 115.00        | 32              |
| 04                                                                 | 129.37         | 18              | 115.00        | 33              |
| 05                                                                 | 138.97         | 19              | 115.00        | 34              |
| 06                                                                 | 148.56         | 20              | 115.00        | 35              |
| 07                                                                 | 124.89         | 21              | 115.00        | 36              |
| 08                                                                 | 141.52         | 22              | 116.44        | 37              |
| 09                                                                 | 135.58         | 23              | 113.56        | 38              |
| 10                                                                 | 125.00         | 24              | 115.00        | 39              |
| 11                                                                 | 125.00         | 25              | 115.00        |                 |
| 12                                                                 | 125.00         | 26              | 115.00        |                 |
| 13                                                                 | 115.00         | 27              | 115.00        |                 |
| 14                                                                 | 115.00         | 28              | 115.00        |                 |
| 15                                                                 | 115.00         | 29              | 106.09        |                 |
| Lot Centre Commercial 1                                            |                | 1 263.79        |               |                 |
| Lot Centre Commercial 2                                            |                | 1 286.62        |               |                 |
| Equipement 3 Sera cédés sans droit à l'indemnisation (article 5.2) |                | 484.37          |               |                 |
| Equipement 4 Sera cédés sans droit à l'indemnisation (article 5.2) |                | 279.71          |               |                 |

Les Lots L'équipements 3 et 4 Seront cédés sans droit à l'indemnisation (article 5.2)  
-Toutes les Rue et parking seront Aménagés et cédés gratuitement à la Commune.