


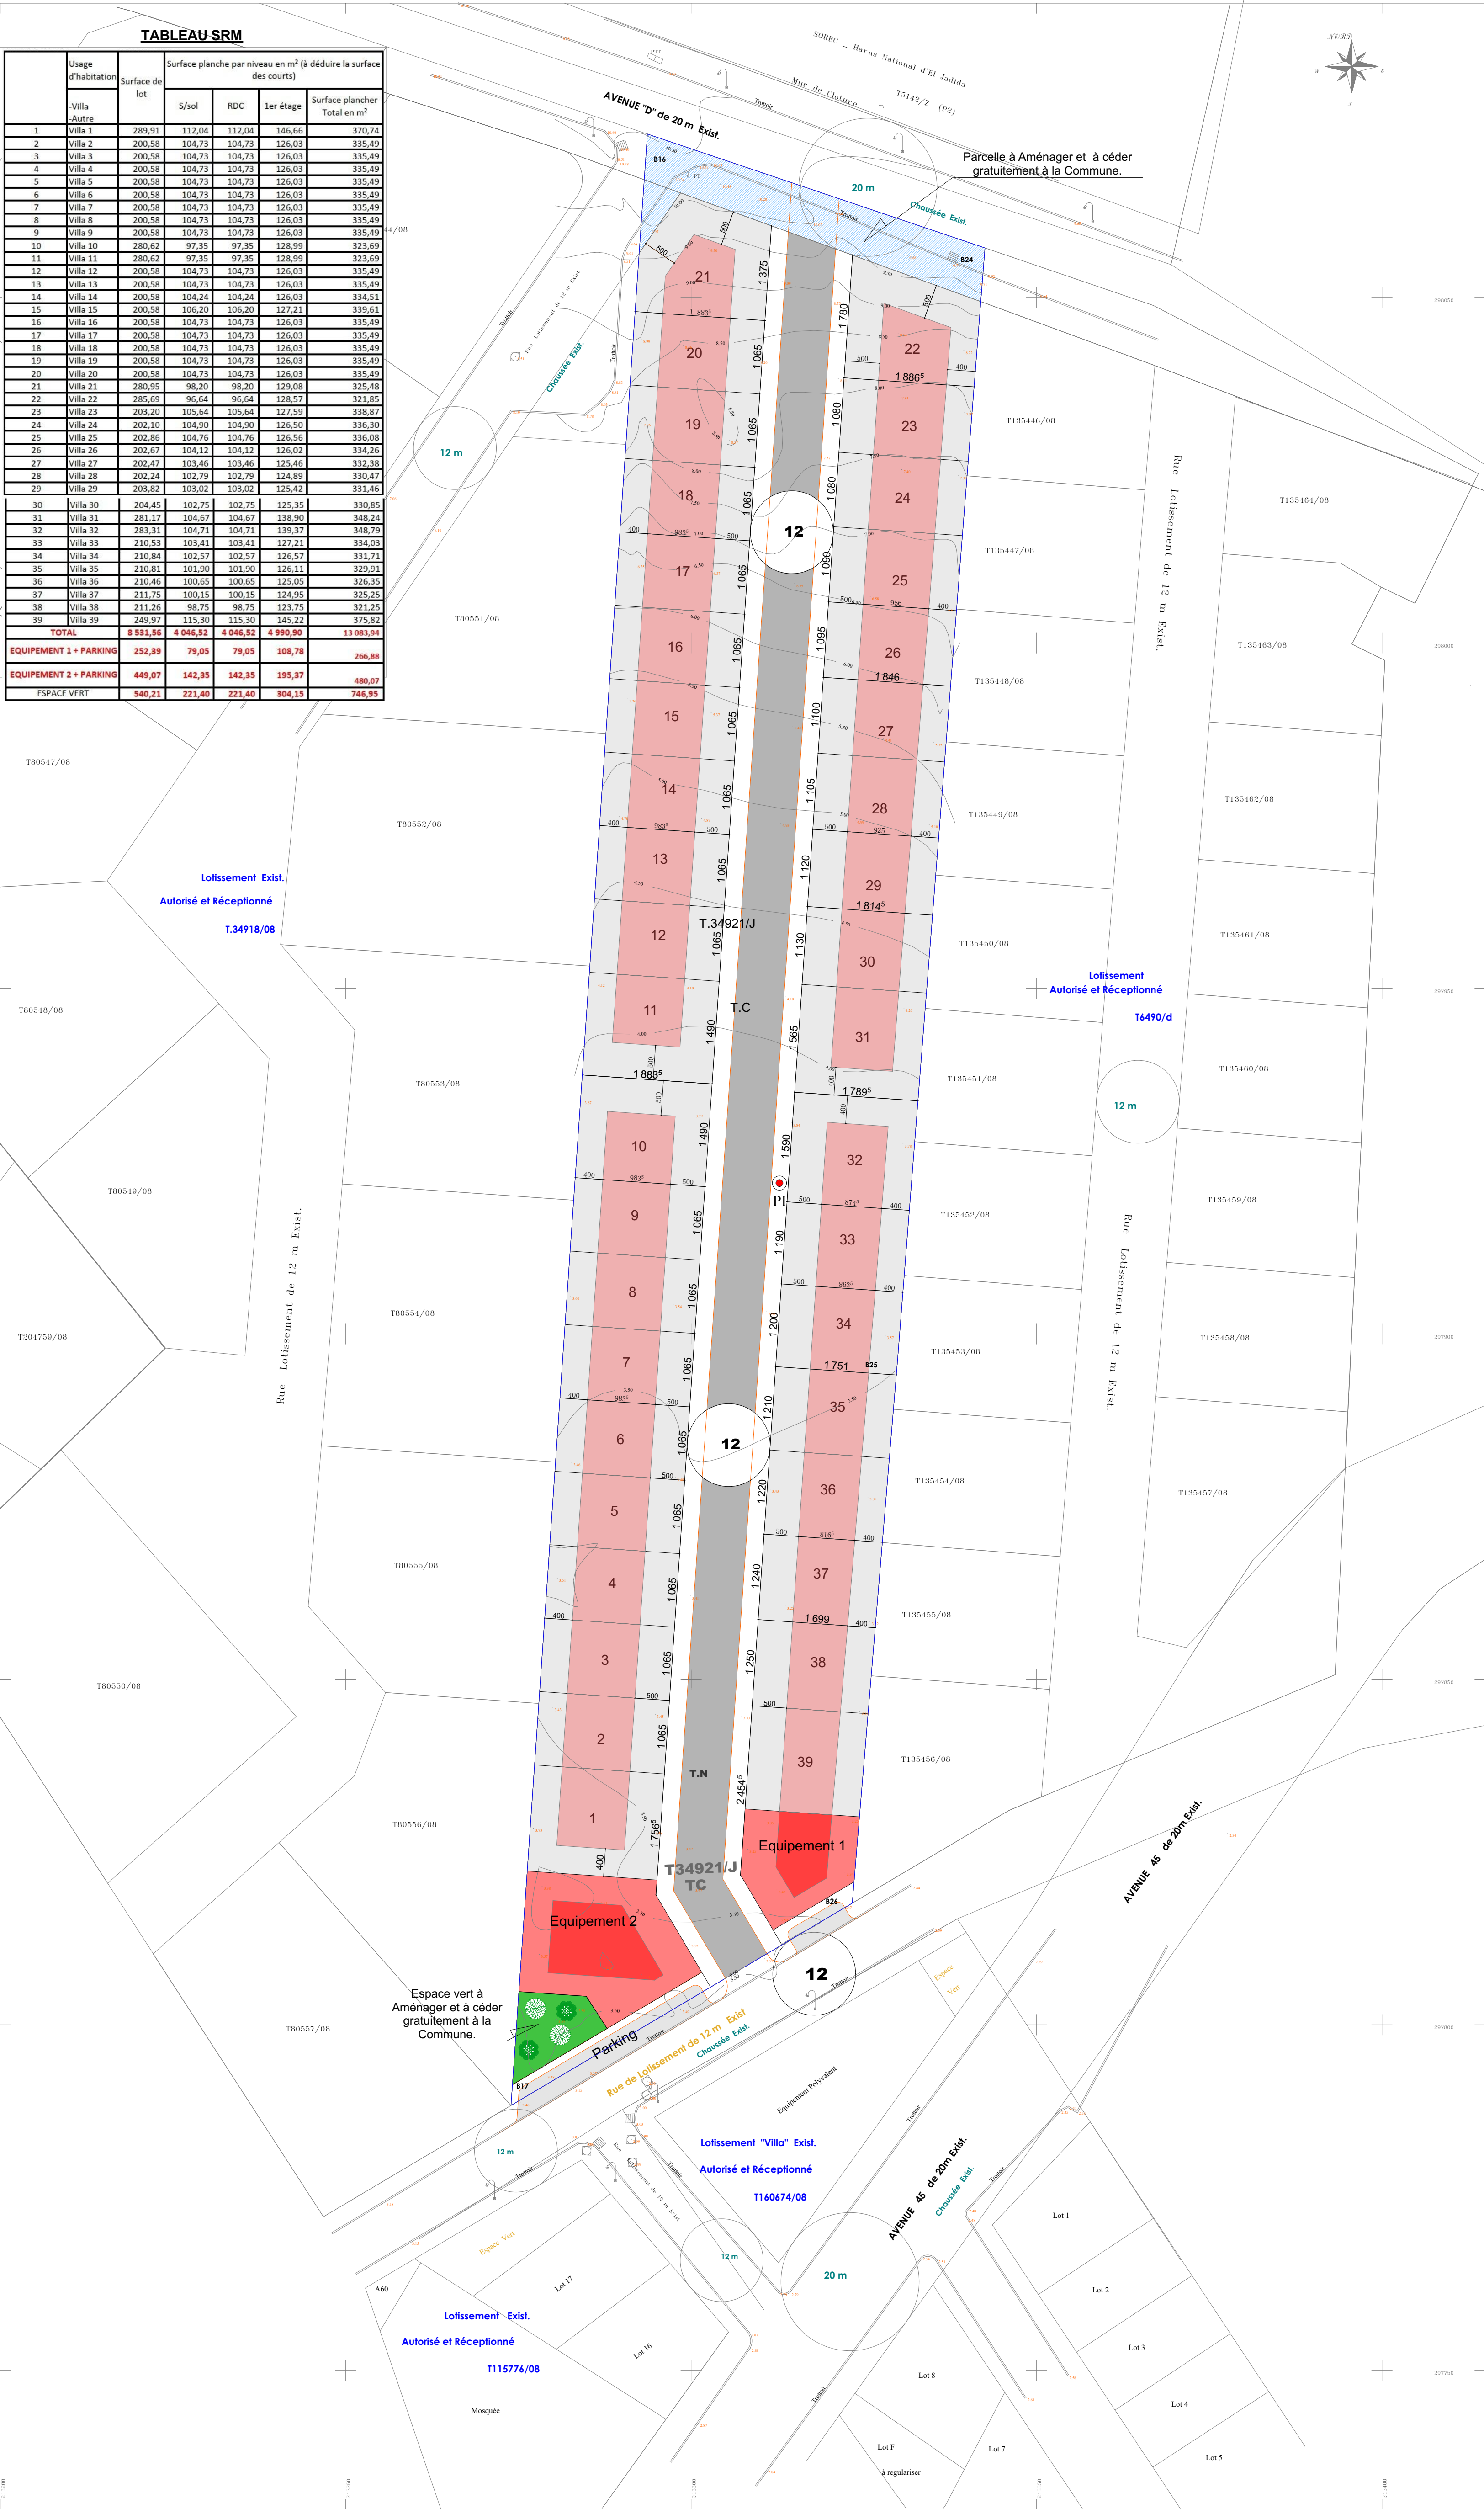

ROYAUME DU MAROC
PROVINCE D'EL JADIDA
COMMUNE TERRITORIALE EL JADIDA

MAITRE D'OUVRAGE :
ABDALLAH AMROUCH Et Consorts
Représentée Par : STE TERRA SIDI RAHAL SARL
Gérant : M. ISMAIL AZENNAR

PROJET :
LOTISSEMENT EN VILLA
SIS : Pré dite AMROUCHE 1, EL JADIDA
T.F 34 921 / J

PLANS :

LE MAITRE D'OUVRAGE EST TENU DE PRESENTER A L'ARCHITECTE DES PLANS DE BETON ARME ETABLIS PAR UN BUREAU D'ETUDE AGREE ET INFORMER L'ARCHITECTE DE LA DATE DU COMMENCEMENT DES TRAVAUX .

PLANCHE N° :
1 / 1

ABconcept
BELARBI ANASS
Architecte d'EN.A
Bureau N° 1 Bld. 1° Residence Essafie
EL JADIDA
Tél : 0523 39 43 35 Fax : 08 08 35 95 43

MODIFICATION :
ECHELLE : 1/500
DATE LE : 04-05-2026


Légende sécurité incendie

PI : Poteau d'Incendie
(100mm de diamètre)

TABLEAU DE CONTENANCE					
N°LOT	SUPERFICIE m²	N°LOT	SUPERFICIE m²	N°LOT	SUPERFICIE m²
Villa 1	289.91	Villa 16	200.58	Villa 31	281.17
Villa 2	200.58	Villa 17	200.58	Villa 32	283.31
Villa 3	200.58	Villa 18	200.58	Villa 33	210.53
Villa 4	200.58	Villa 19	200.58	Villa 34	210.84
Villa 5	200.58	Villa 20	200.58	Villa 35	210.81
Villa 6	200.58	Villa 21	280.95	Villa 36	210.46
Villa 7	200.58	Villa 22	285.69	Villa 37	211.75
Villa 8	200.58	Villa 23	203.20	Villa 38	211.26
Villa 9	200.58	Villa 24	202.10	Villa 39	249.97
Villa 10	280.62	Villa 25	202.86	Equipement 1 Parking	252.39
Villa 11	280.62	Villa 26	202.67	Equipement 2 Parking	449.07
Villa 12	200.58	Villa 27	202.47	Espace Vert	151.99
Villa 13	200.58	Villa 28	202.24		
Villa 14	200.58	Villa 29	203.82		
Villa 15	200.58	Villa 30	204.45		

L'équipement et les espaces verts sont à céder à la collectivité locale sans droit à l'indemnisation (article 5.2)

PROJET

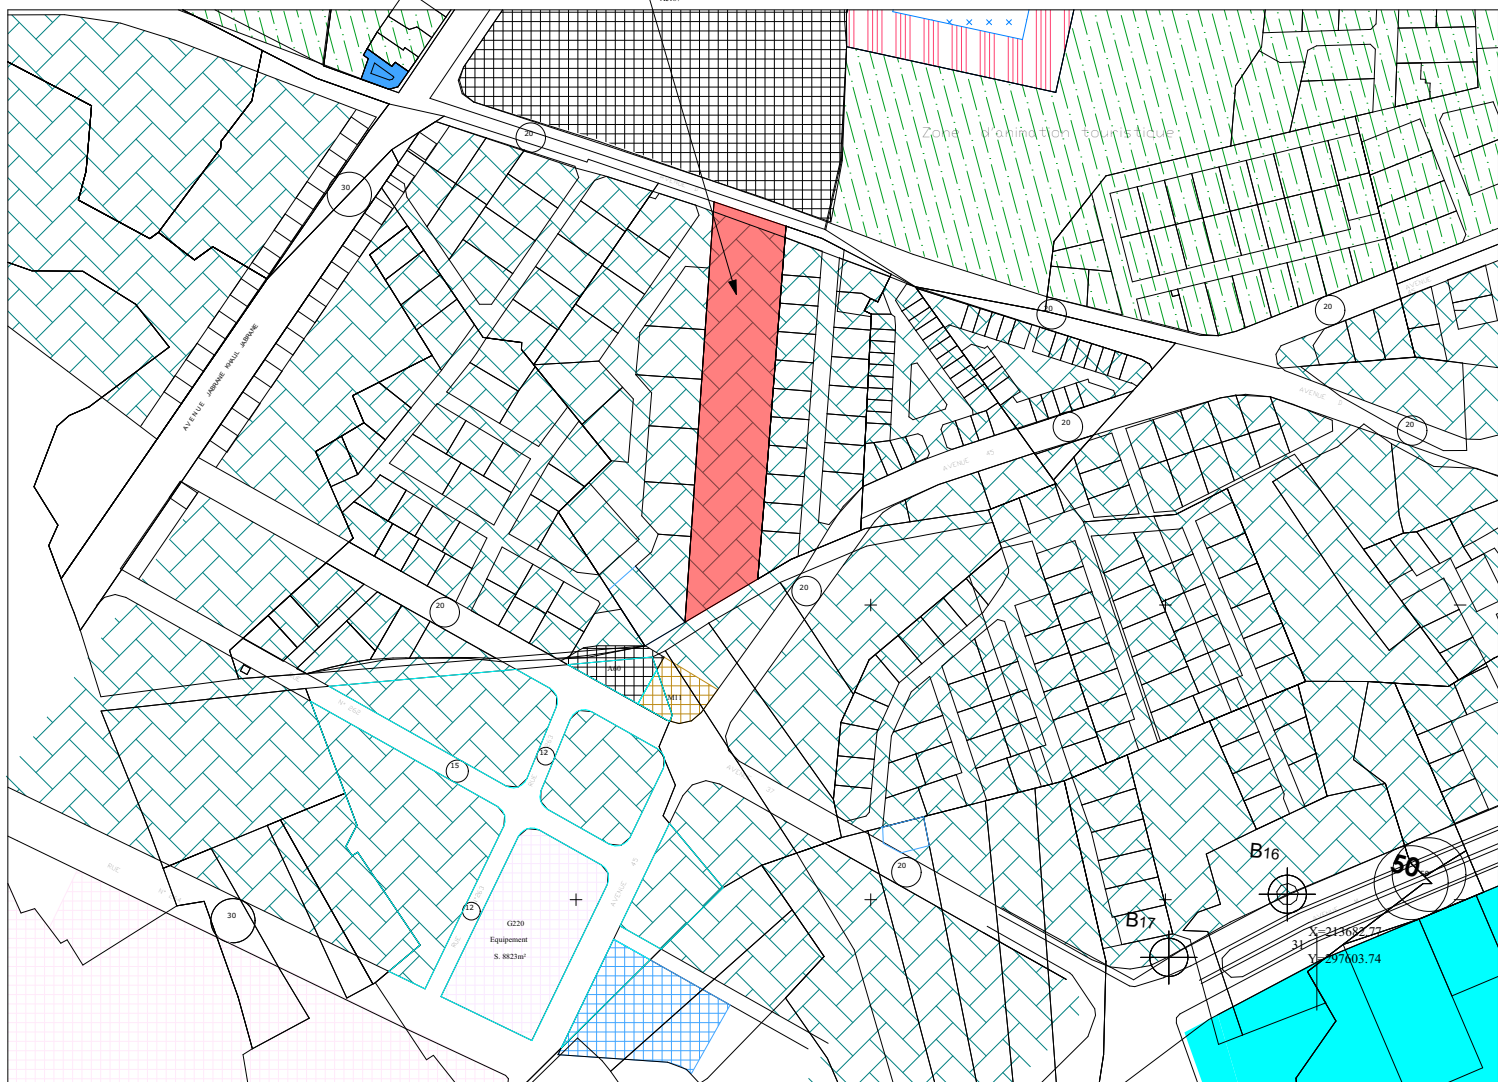

PLAN SITUATION

LE JADIDA APPROUVE
Sign par ANASS BELARBI
le 26/06/2026

ARCHITECTE
Sign par ANASS BELARBI
le 16/06/2026

PRESIDENT DE LA COMMUNE
Sign par JAMAL BENRABIA
COMMUNE D'EL JADIDA
le 10/08/2026