


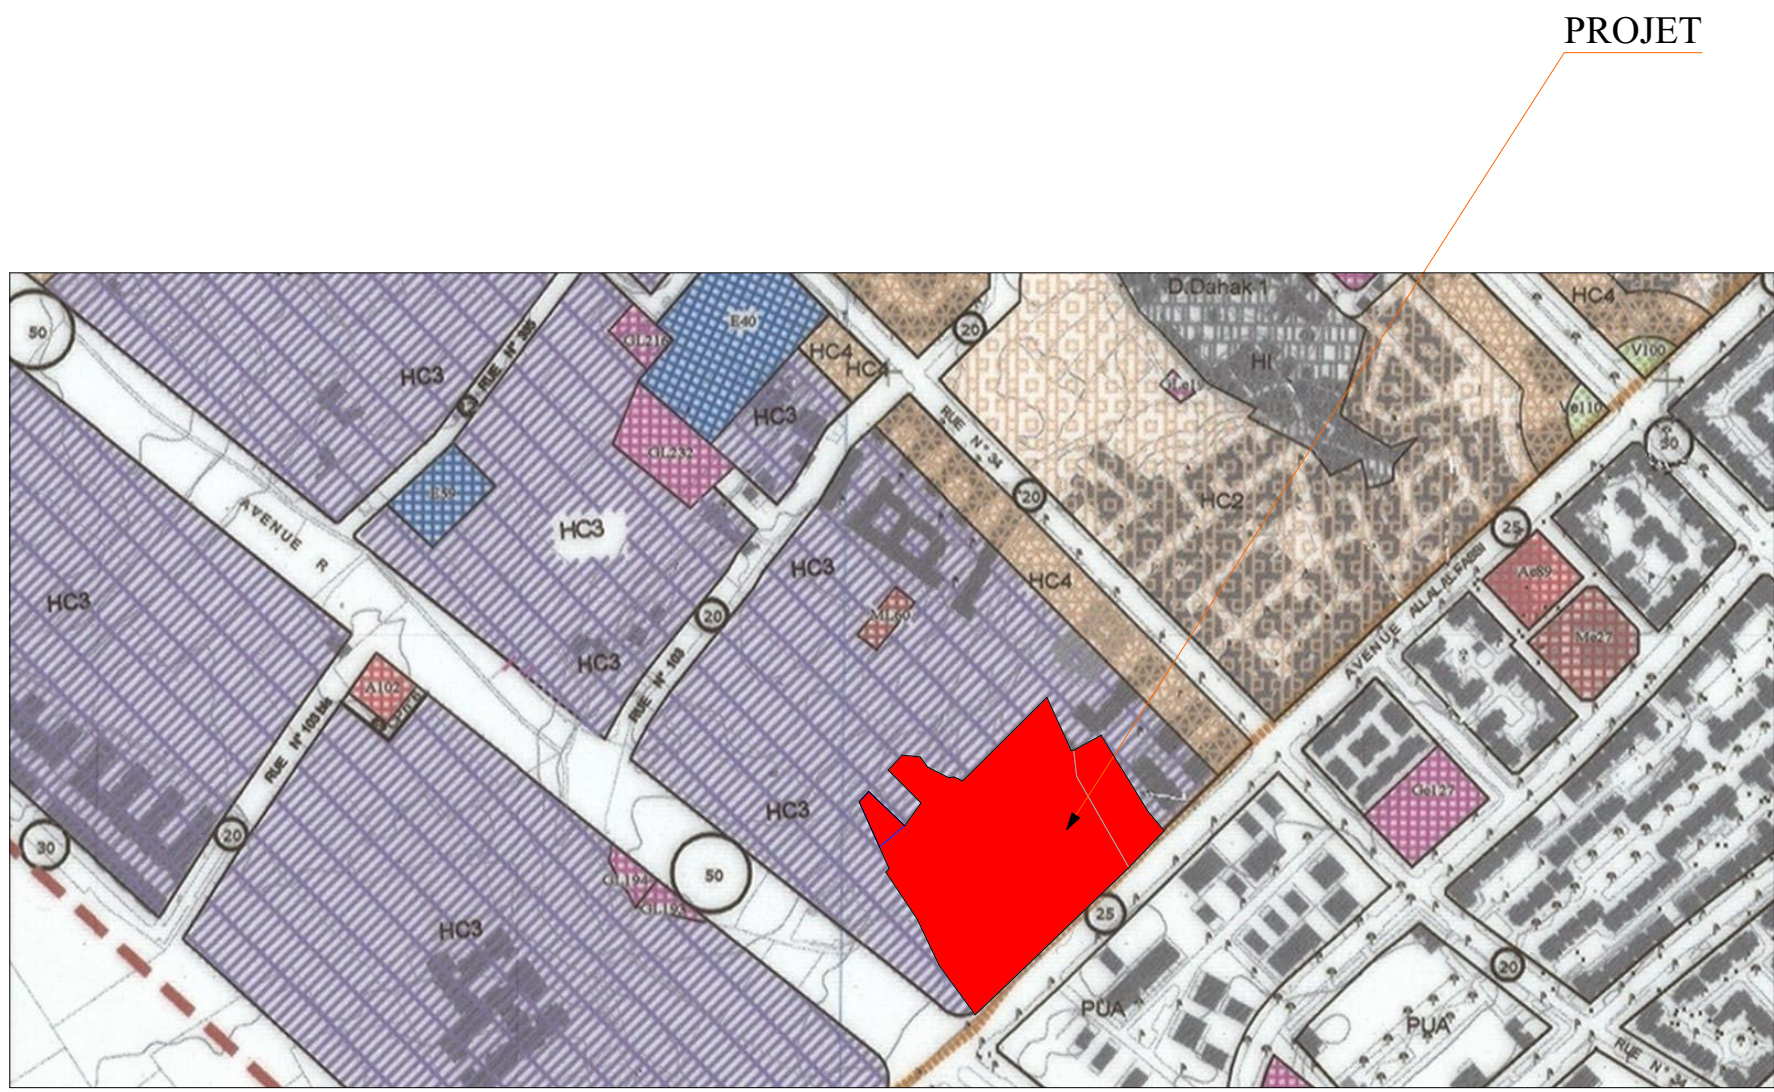

EXTRAIT P.A

TABLEAU DE CONTENANCE


LOTS R+3									
N°LOT	SUPERFICIE m²	N°LOT	SUPERFICIE m²	N°LOT	SUPERFICIE m²	N°LOT	SUPERFICIE m²	N°LOT	SUPERFICIE m²
1 R+3	164.61	13 R+3	162.52	25 R+3	155.50	37 R+3	155.07	49 R+3	168.42
2 R+3	153.76	14 R+3	150.65	26 R+3	155.40	38 R+3	161.87	Equipement 1 +Place + Parking	337.80
3 R+3	162.50	15 R+3	162.51	27 R+3	155.06	39 R+3	161.52		
4 R+3	150.65	16 R+3	150.65	28 R+3	155.40	40 R+3	184.49	Equipement 2 +Parking	478.38
5 R+3	162.50	17 R+3	192.21	29 R+3	155.07	41 R+3	149.25		
6 R+3	150.65	18 R+3	178.20	30 R+3	155.40	42 R+3	203.69	Légende sécurité incendie ● PI : Poteau d'Incendie (100mm de diamètre)	
7 R+3	162.50	19 R+3	182.10	31 R+3	155.07	43 R+3	206.85		
8 R+3	150.65	20 R+3	164.67	32 R+3	155.40	44 R+3	160.76		
9 R+3	162.49	21 R+3	186.93	33 R+3	155.07	45 R+3	160.54		
10 R+3	150.64	22 R+3	215.69	34 R+3	155.40	46 R+3	151.94		
11 R+3	162.50	23 R+3	290.89	35 R+3	155.07	47 R+3	151.43		
12 R+3	150.65	24 R+3	155.74	36 R+3	155.40	48 R+3	150.93		

Légende sécurité incendie

PI : Poteau d'Incendie
(100mm de diamètre)



	AUTORISEE
	MODIFIE

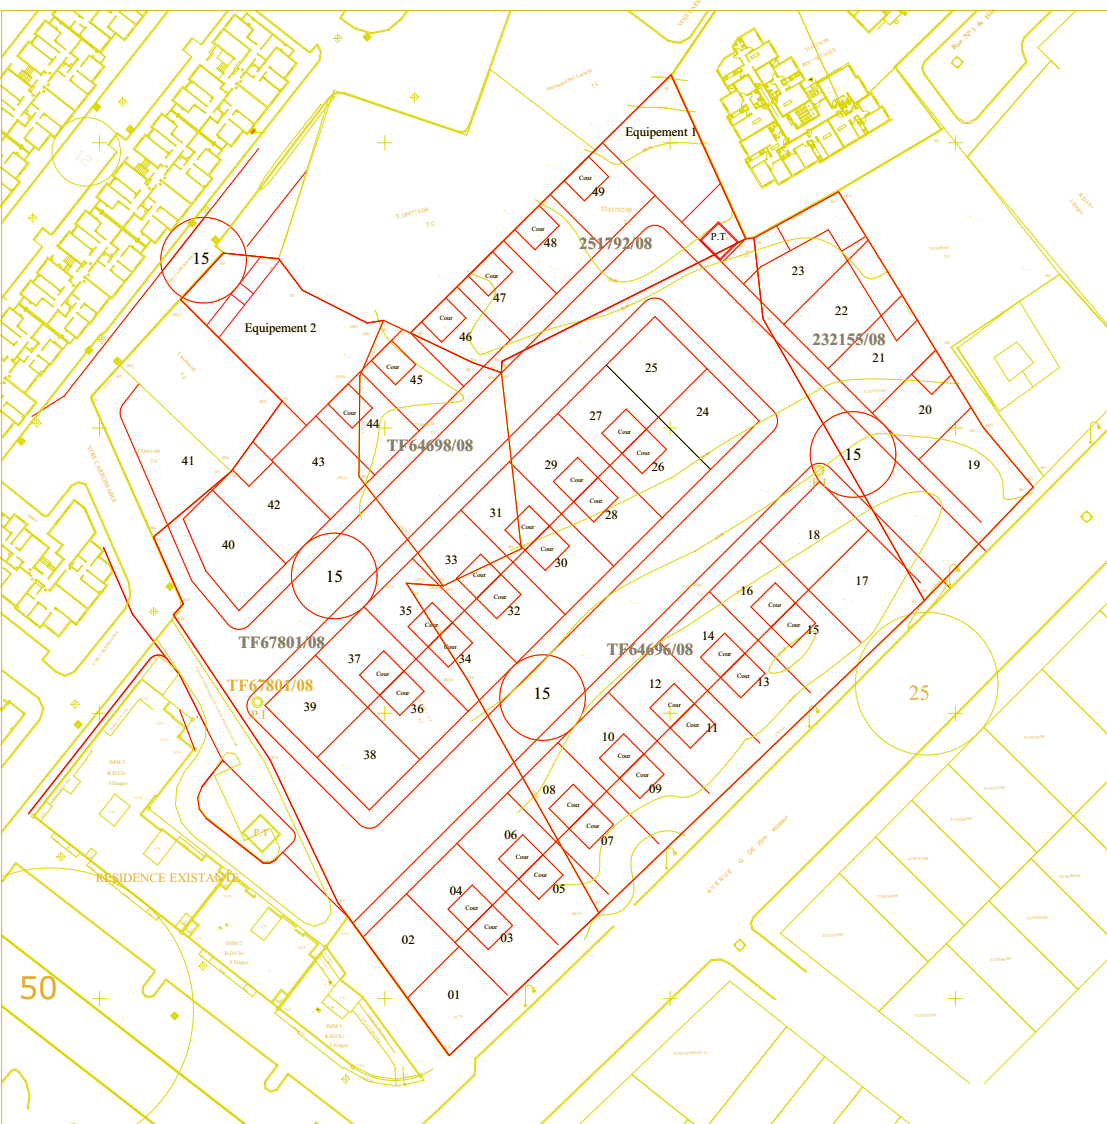

PLAN AUTORISE MODIFIE

ROYAUME DU MAROC
PROVINCE EL JADIDA
COMMUNE TERRITORIALE D'EL JADIDA

MAITRE D'OUVRAGE :
STE VIVE BATIMENT S.A.R.L.A.U
Représenté par : EL KAİM-BİLLAH AHMED

PROJET :
LOTISSEMENT ANTALYA EN R+3
MODIFICATION SUITE LA DECISION N° 963 du 31-12-2025
Sis : P16 DITE : "ARD HYOUTE LOUAOUCHI" "HAIT HAJ MOHAMED"
"ARD EL MATAR" "BLED MADANI" ET "ARD HATTA" "ARD EL KRIMATE-EL JADIDA-
T.F 251 792/08 T.F 64 698 / 08 T.F 232 155/08 T.F 64 696/08
T.F 67 801/08 ET T.F 270 661/08

PLANS.

PLAN N° :
1 / 1

LE MAITRE D'OUVRAGE EST TENU
DE PRESENTER A L'ARCHITECTE LE
TECHNIQUE VRD ETABLI PAR UN
BUREAU D'ETUDE AGREE, ET INFORMER
L'ARCHITECTE DE LA DATE DU
COMMENCEMENT DES TRAVAUX.

MODIFICATION :
ECHELLE : 1/500
DATE LE : 03-12-2025

BELARBI ANASS
Architecte d'E.N.A.
Bureau n°1 Bloc "D" Residence Essafec
EL JADIDA
Tél: 0523 39 43 35 Fax: 08 08 33 95 43

N.B : -Les équipements sont à céder sans droit, conformément à l'article 5.2 du règlement d'aménagement.

-Les rues et voies seront aménagées et cédées gratuitement à la commune.

TABLEAU SRM

Usage d'habitation	Econometrique -Villa -Touristique -Industriel -Autre	Surface de lot	Surface plancher						
			RDC	MEZZANIN E	Surface plancher commerce en m²	1er étage	2ème étage	3ème étage	
			Surface plancher Total en m²						
1	LOT 1 R+3	164.61	164.61	82.31	246.92	173.61	173.61	173.61	520.83
2	LOT 2 R+3	153.76	153.76	76.88	230.64	160.76	160.76	160.76	482.28
3	LOT 3 R+3	162.50	162.50	81.25	243.75	140.50	140.50	140.50	421.50
4	LOT 4 R+3	150.65	150.65	75.33	225.98	128.65	128.65	128.65	385.95
5	LOT 5 R+3	162.50	162.50	81.25	243.75	140.50	140.50	140.50	421.50
6	LOT 6 R+3	150.65	150.65	75.33	225.98	128.65	128.65	128.65	385.95
7	LOT 7 R+3	162.50	162.50	81.25	243.75	140.50	140.50	140.50	421.50
8	LOT 8 R+3	150.65	150.65	75.33	225.98	128.65	128.65	128.65	385.95
9	LOT 9 R+3	162.49	162.49	81.25	243.74	140.49	140.49	140.49	421.47
10	LOT 10 R+3	150.64	150.64	75.32	225.96	128.64	128.64	128.64	385.92
11	LOT 11 R+3	162.50	162.50	81.25	243.75	140.50	140.50	140.50	421.50
12	LOT 12 R+3	150.65	150.65	75.33	225.98	128.65	128.65	128.65	385.95
13	LOT 13 R+3	162.52	162.52	81.26	243.78	140.52	140.52	140.52	421.56
14	LOT 14 R+3	150.65	150.65	75.33	225.98	128.65	128.65	128.65	385.95
15	LOT 15 R+3	162.51	162.51	81.26	243.77	140.51	140.51	140.51	421.53
16	LOT 16 R+3	150.65	150.65	75.33	225.98	128.65	128.65	128.65	385.95
17	LOT 17 R+3	192.21	192.21	96.10	288.31	209.21	209.21	209.21	627.63
18	LOT 18 R+3	178.20	178.20	89.10	267.30	196.00	196.00	196.00	588.00
19	LOT 19 R+3	182.10	182.10	91.05	273.15	199.10	199.10	199.10	577.30
20	LOT 20 R+3	164.67	164.67	82.33	247.00	146.00	146.00	146.00	430.00
21	LOT 21 R+3	186.93	186.93	93.46	280.39	168.93	168.93	168.93	506.79
22	LOT 22 R+3	215.69	215.69	107.85	323.54	166.16	166.16	166.16	498.48
23	LOT 23 R+3	290.89	290.89	145.45	436.34	154.00	154.00	154.00	402.00
24	LOT 24 R+3	155.74	155.74	77.87	233.61	171.74	171.74	171.74	515.22
25	LOT 25 R+3	155.50	155.50	77.75	233.25	171.50	171.50	171.50	514.50
26	LOT 26 R+3	155.40	155.40	77.70	233.10	133.40	133.40	133.40	402.20
27	LOT 27 R+3	155.06	155.06	77.53	232.99	133.06	133.06	133.06	399.18
28	LOT 28 R+3	155.40	155.40	77.70	233.10	133.40	133.40	133.40	400.20
29	LOT 29 R+3	155.07	155.07	77.54	232.61	133.07	133.07	133.07	399.21
30	LOT 30 R+3	155.40	155.40	77.70	233.10	133.40	133.40	133.40	400.20
31	LOT 31 R+3	155.07	155.07	77.54	232.61	133.07	133.07	133.07	399.21
32	LOT 32 R+3	155.40	155.40	77.70	233.10	133.40	133.40	133.40	400.20
33	LOT 33 R+3	155.07	155.07	77.54	232.61	133.07	133.07	133.07	399.21
34	LOT 34 R+3	155.40	155.40	77.70	233.10	133.40	133.40	133.40	400.20
35	LOT 35 R+3	155.07	155.07	77.54	232.61	133.07	133.07	133.07	399.21
36	LOT 36 R+3	155.40	155.40	77.70	233.10	133.40	133.40	133.40	400.20
37	LOT 37 R+3	155.07	155.07	77.54	232.61	133.07	133.07	133.07	399.21
38	LOT 38 R+3	161.87	161.87	80.93	243.80	177.87	177.87	177.87	513.61
39	LOT 39 R+3	161.52	161.52	80.76	243.28	177.52	177.52	177.52	512.56
40	LOT 40 R+3	184.49	184.49	92.24	276.73	203.49	203.49	203.49	610.47
41	LOT 41 R+3	149.25	149.25	74.62	223.87	164.25	164.25	164.25	409.75
42	LOT 42 R+3	203.69	203.69	101.84	305.53	183.30	183.30	183.30	549.90
43	LOT 43 R+3	206.85	206.85	103.42	310.27	167.62	167.62	167.62	520.86
44	LOT 44 R+3	160.76	160.76	80.38	241.14	137.76	137.76	137.76	413.28
45	LOT 45 R+3	160.54	160.54	80.27	240.81	137.54	137.54	137.54	412.82
46	LOT 46 R+3	151.94	151.94	75.97	227.91	128.94	128.94	128.94	386.82
47	LOT 47 R+3	151.43	151.43	75.71	227.14	128.43	128.43	128.43	385.59
48	LOT 48 R+3	150.93	150.93	75.46	226.39	127.93	127.93	127.93	383.79
49	LOT 49 R+3	168.42	168.42	84.21	252.63	146.42	146.42	146.42	439.26
EQUIPEMENT 1 Place		337.80	188.79	94.25	283.04	196.45	196.45	196.45	589.35
1	EQUIPEMENT 2 Parking	478.38	478.38	239.19	717.57	488.38	488.38	488.38	1 465.14

APPROUVE
Sign par JAMAL BEURABIA
EL JADIDA
le 14/03/2026

ARCHITECTE
Sign par ANASS BELARBI
le 27/02/2026

PRESIDENT DE LA COMMUNE
Sign par JAMAL BEURABIA
COMMUNE D'EL JADIDA
le 22/04/2026