





PROJET

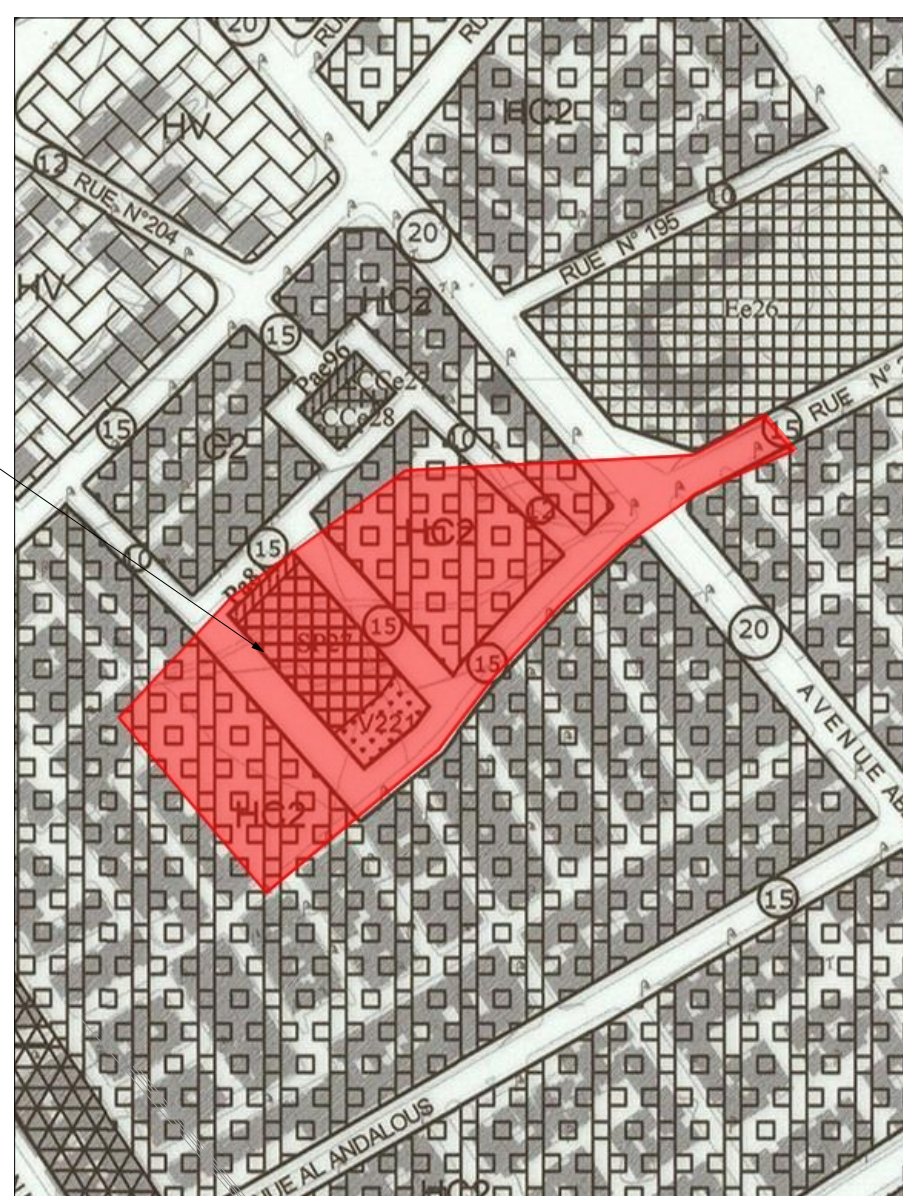

**EXTRAIT DE PLAN
D'AMENAGEMENT**

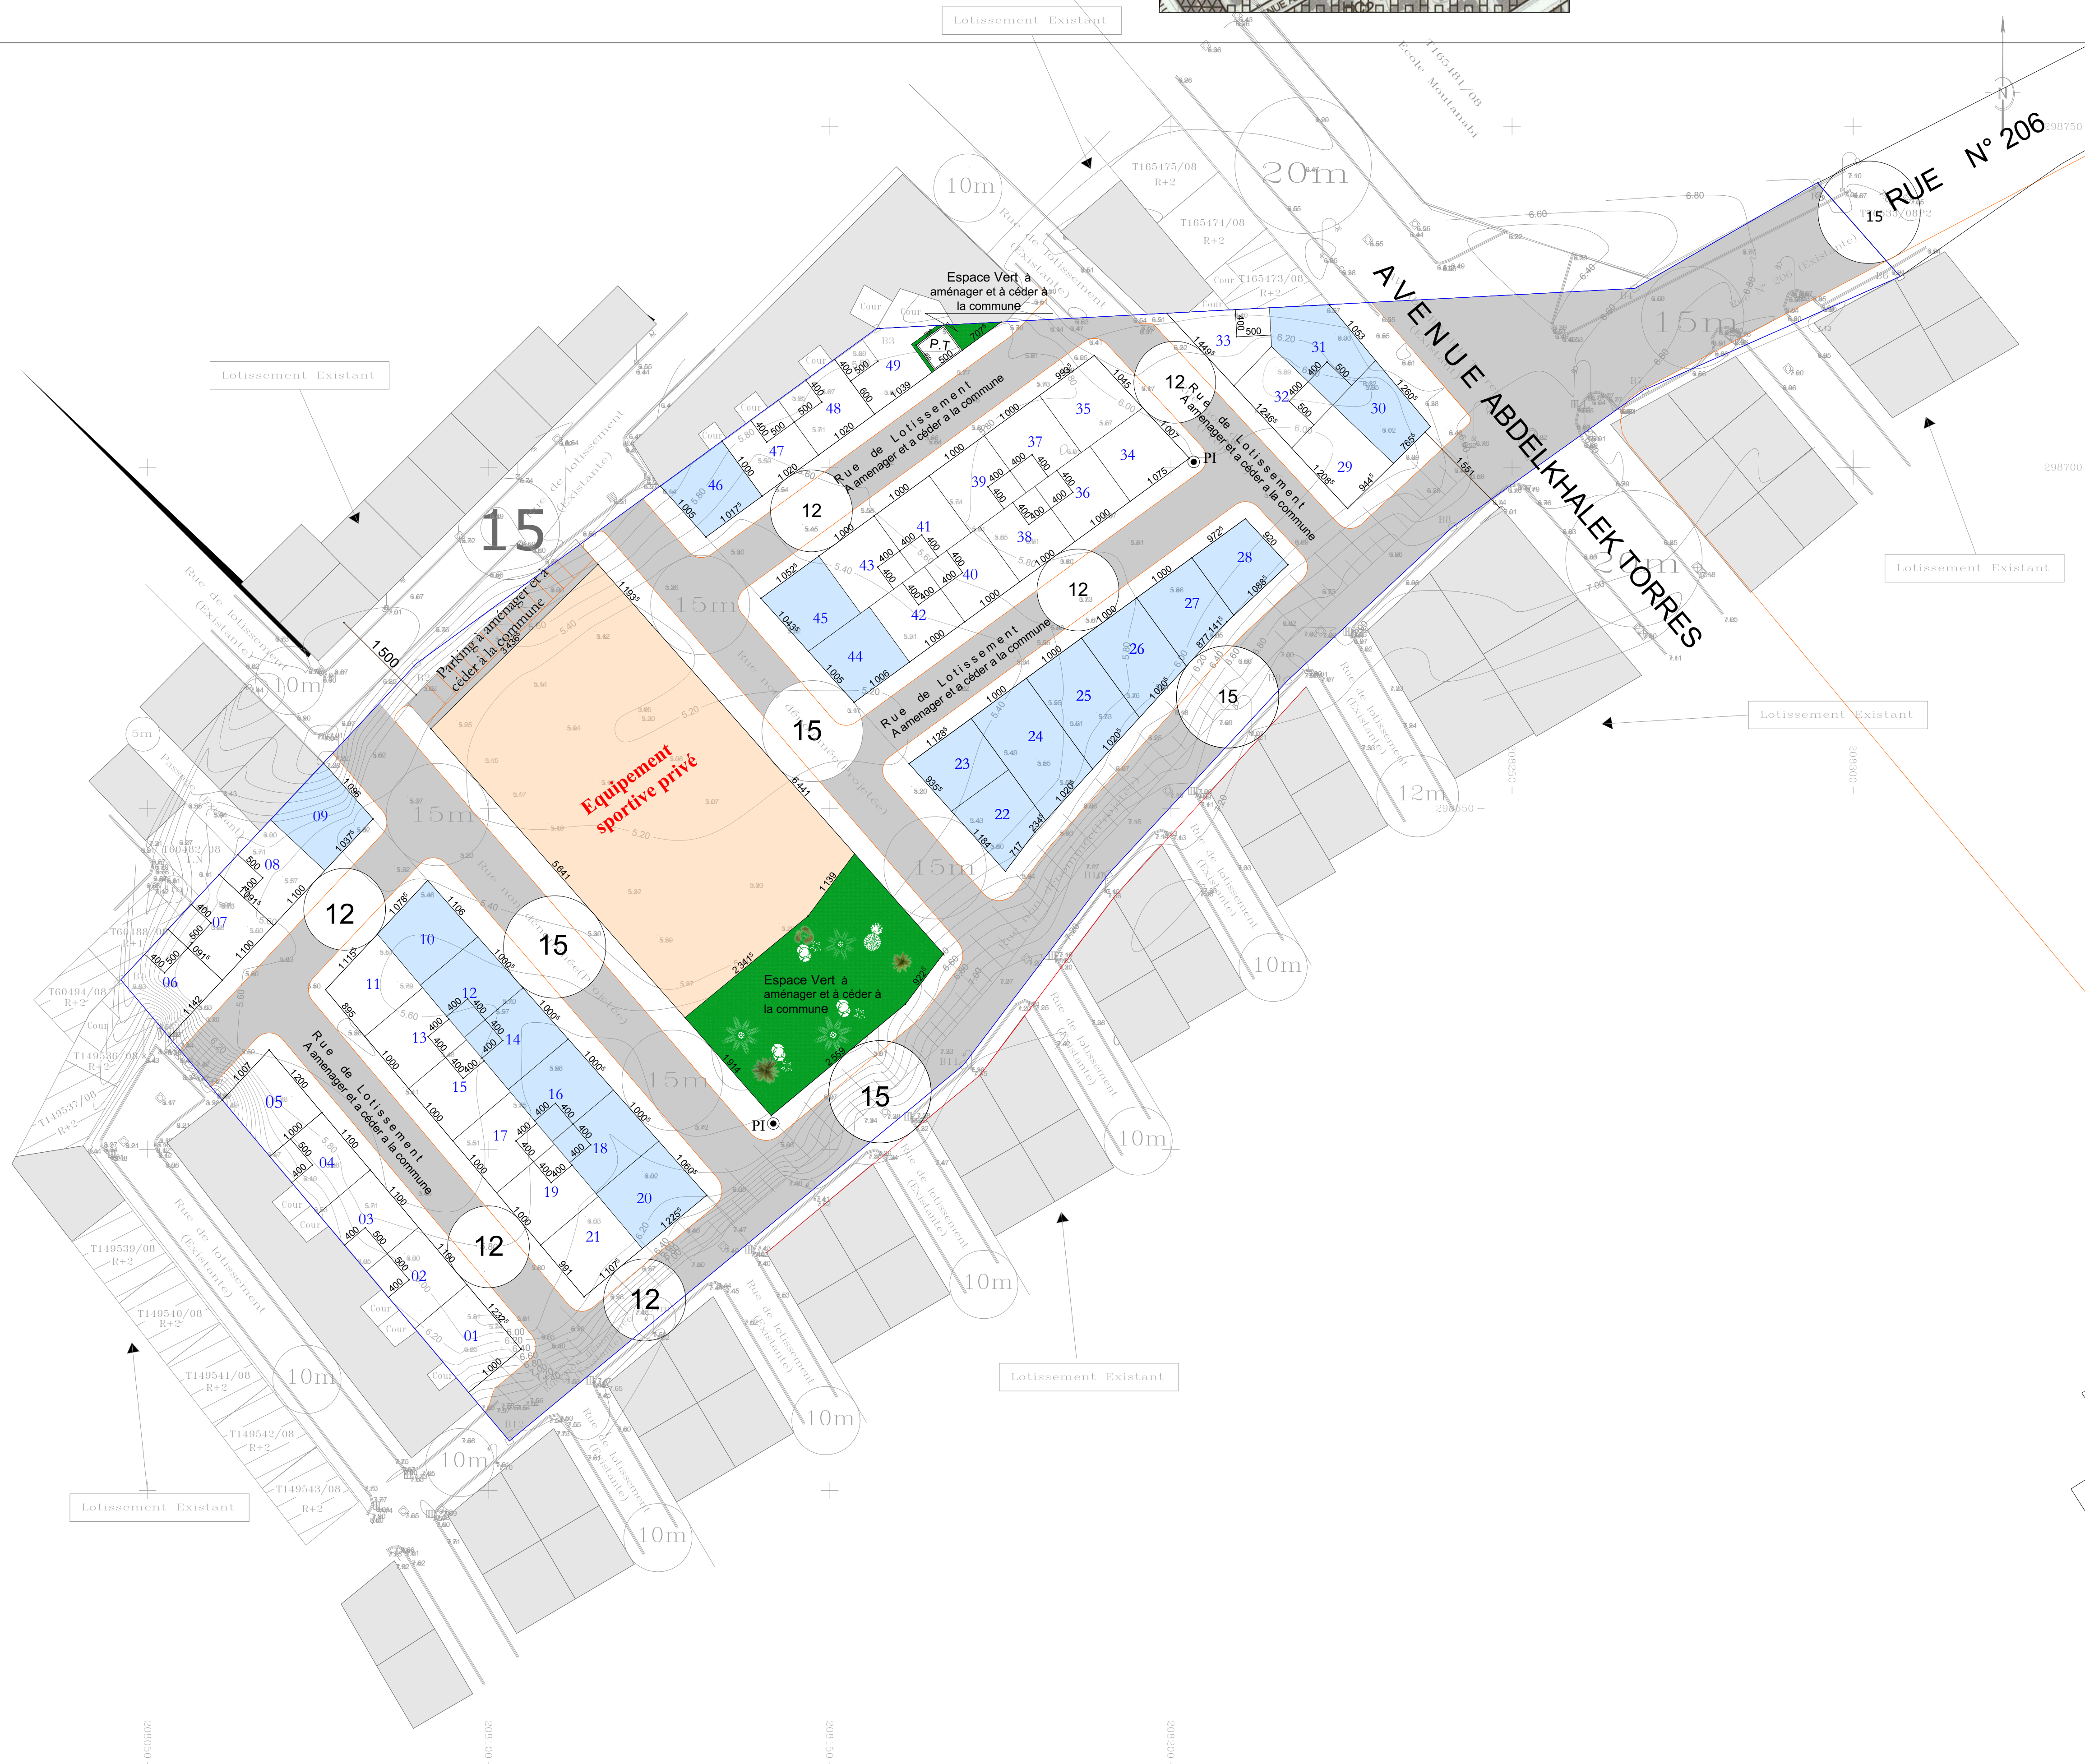

ROYAUME DU MAROC
PROVINCE D'EL JADIDA
COMMUNE TERRITORIALE EL JADIDA

MAITRE D'OUVRAGE :

STE DINH SARL
Représentée par : Mr GUENNOUN DAFIR

PROJET :


LOTISSEMENT EN R+2
Pté dite " ARD ESSANIA " Douar El bahara -EL JADIDA-
T.F N ° : 132 574 /08

PLANS.

LE MAITRE D'OUVRAGE EST TENU
DE PRESENTER A L'ARCHITECTE DES
PLANS DE BETON ARME ETABLIS PAR UN
BUREAU D'ETUDE AGREE, ET INFORMER
L'ARCHITECTE DE LA DATE DU
COMMENCEMENT DES TRAVAUX.

PLANCHE N° .

111

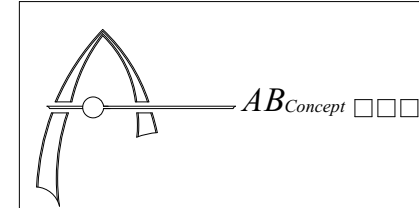

BELARBI ANASS
Architecte d'E.N.A
Bureau n° 1 Bloc " D " Résidence Essafae
-EL JADIDA-
tel : 0523 39 43 35 Fax : 08 08 35 95 43

MODIFICATION ·

ECHELLE : 1/500

DATE LE : 29/06/2026

N°LOT R+2	SUPERFICIE m²	N°LOT R+2	SUPERFICIE m²	N°LOT R+2	SUPERFICIE m²	N°LOT R+2	SUPERFICIE m²
1 r+ch habitation	122.82	15 r+ch habitation	110.76	29 r+ch commerce	110.71	43 r+ch habitation	103.80
2 r+ch habitation	110.00	16 r+ch commerce	116.12	30 commerce	103.96	44 r+ch commerce	105.62
3 r+ch habitation	110.00	17 r+ch habitation	110.76	31 r+ch commerce	136.94	45 r+ch commerce	103.79
4 r+ch habitation	110.00	18 commerce	118.62	32 r+ch habitation	103.82	46 r+ch commerce	106.77
5 r+ch habitation	114.02	19 r+ch habitation	110.76	33 commerce	100.58	47 r+ch habitation	101.98
6 r+ch habitation	117.06	20 r+ch commerce	127.86	34 r+ch habitation	101.60	48 r+ch habitation	101.98
7 r+ch habitation	119.83	21 r+ch habitation	110.26	35 r+ch habitation	109.50	49 r+ch habitation	108.62
8 r+ch habitation	120.06	22 r+ch commerce	102.36	36 r+ch habitation	100.00		
9 r+ch commerce	118.85	23 r+ch commerce	100.71	37 r+ch habitation	103.80		
10 r+ch commerce	113.07	24 r+ch commerce	175.03	38 r+ch habitation	100.00		
11 r+ch commerce	106.46	25 r+ch commerce	154.57	39 r+ch habitation	103.80		
12 r+ch habitation	111.11	26 r+ch commerce	134.11	40 r+ch habitation	100.00		
13 r+ch habitation	110.76	27 r+ch commerce	113.73	41 r+ch habitation	103.80		
14 r+ch commerce	113.62	28 r+ch commerce	100.91	42 r+ch habitation	100.00		
Equipeement sportive privé			1978.54				
Espace Vert+ Parking Secours incendie+ Gde Ssm droit à l'indemnisation (Suite l'article 5.2 du			850.84				

- Espace Vert et Parking Seront aménagés et Cédés Sans droit à l'indemnisation
(Suite l'article 5.2 du règlement d'aménagement

[illegible]

Légende sécurité incendie

- PI : Poteau d'Incendie
(100mm de diamètre)

ARCHITECTE
Signé par ANASS BELARB
le 15/09/2026